

INDEX

A0.0	COVER SHEET
A1.0	FLOOR PLAN
A1.1	LIGHTING AND FLOOR REGISTER LAYOUT
A2.0	ELEVATIONS - STANDARD
A3.0	INTERIOR DETAILS - KITCHEN
A3.1	INTERIOR DETAILS - KITCHEN
A3.2	INTERIOR DETAILS - BATHS
A3.3	INTERIOR DETAILS - MISC
A4.0	SALESLIT PRINT SALESLIT

GENERAL NOTES

1. THIS PACKAGE IS INTENDED TO RELAY DESIGN INTENT AND IS NOT FOR CONSTRUCTION.
2. PLEASE CONTACT ANDY HUTSELL AT ANDY.HUTSELL@CLAYTONHOMES.COM WITH QUESTIONS REGARDING THESE DRAWINGS.

SYMBOLS AND ABBREVIATIONS

CLG	CEILING
DR	DOOR
EF	EXHAUST FAN
FLR	FLOOR
MNT	MOUNT
OPT	OPTIONAL
RAG	RETURN AIR GRILLE
SEP	STANDARD ELECTRIC PANEL
SGD	SLIDING GLASS DOOR

Clayton Built

MODEL NAME: CrossMod_Keeneland_R
MODEL NO.: CrossMod-3258-32-1_Keeneland_R
BOX SIZE: 32' x 58'
MODEL SQ. FT.: 1,635

DATE PRINTED: 9/28/2023


SCALE: N.T.S.
* UNLESS OTHERWISE NOTED

PLAN NO.: CrossMod--3258-32-1_Keeneland_R

SHEET NAME: COVER SHEET

SHEET NO.: A0.0.

File Path:B:\Architecture\CrossMod\DWG Files\3258_KEENELAND\CrossMod--3258-32-1_Keeneland_R.dwg, Last Saved By:Hutsella, Saved Date:9/28/2023 11:20 AM

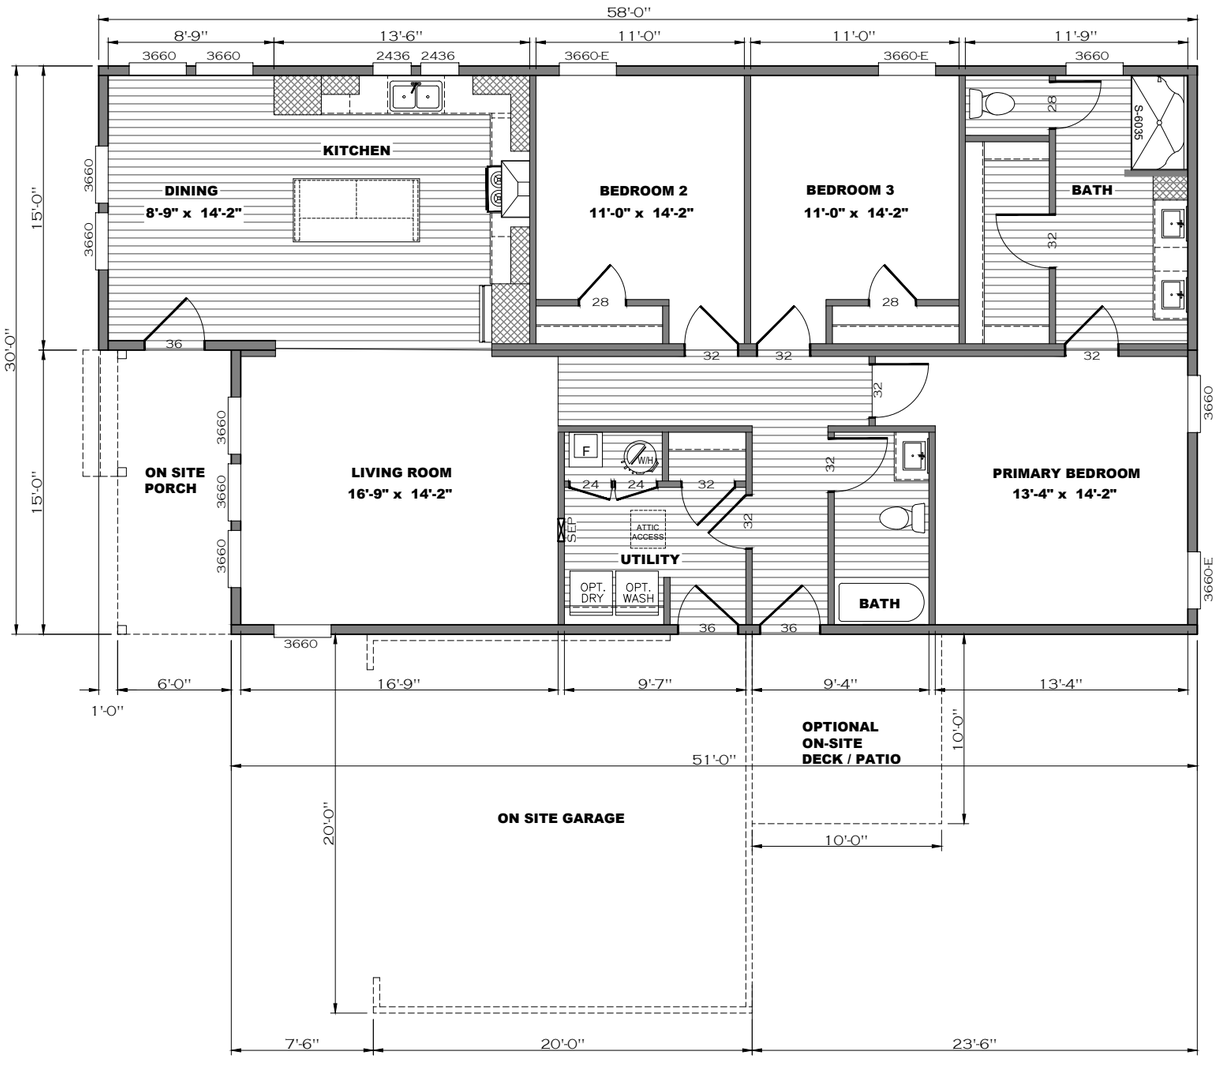


FLOOR PLAN

Clayton Built

MODEL NAME: CrossMod_Keeneland_R
MODEL NO.: CrossMod-3258-32-1_Keeneland_R
BOX SIZE: 32' x 58'
MODEL SQ. FT.: 1,635

DATE PRINTED: 9/28/2023
SCALE: 1/8"=1'
* UNLESS OTHERWISE NOTED
PLAN NO.: CrossMod--3258-32-1_Keeneland_R
SHEET NAME: FLOOR PLAN
SHEET NO.: A1.0.

File Path:B:\Architecture\CrossMod\DWG Files\3258_KEENELAND\CrossMod--3258-32-1_Keeneland_R.dwg, Last Saved By:Hutsella, Saved Date:9/28/2023 11:20 AM

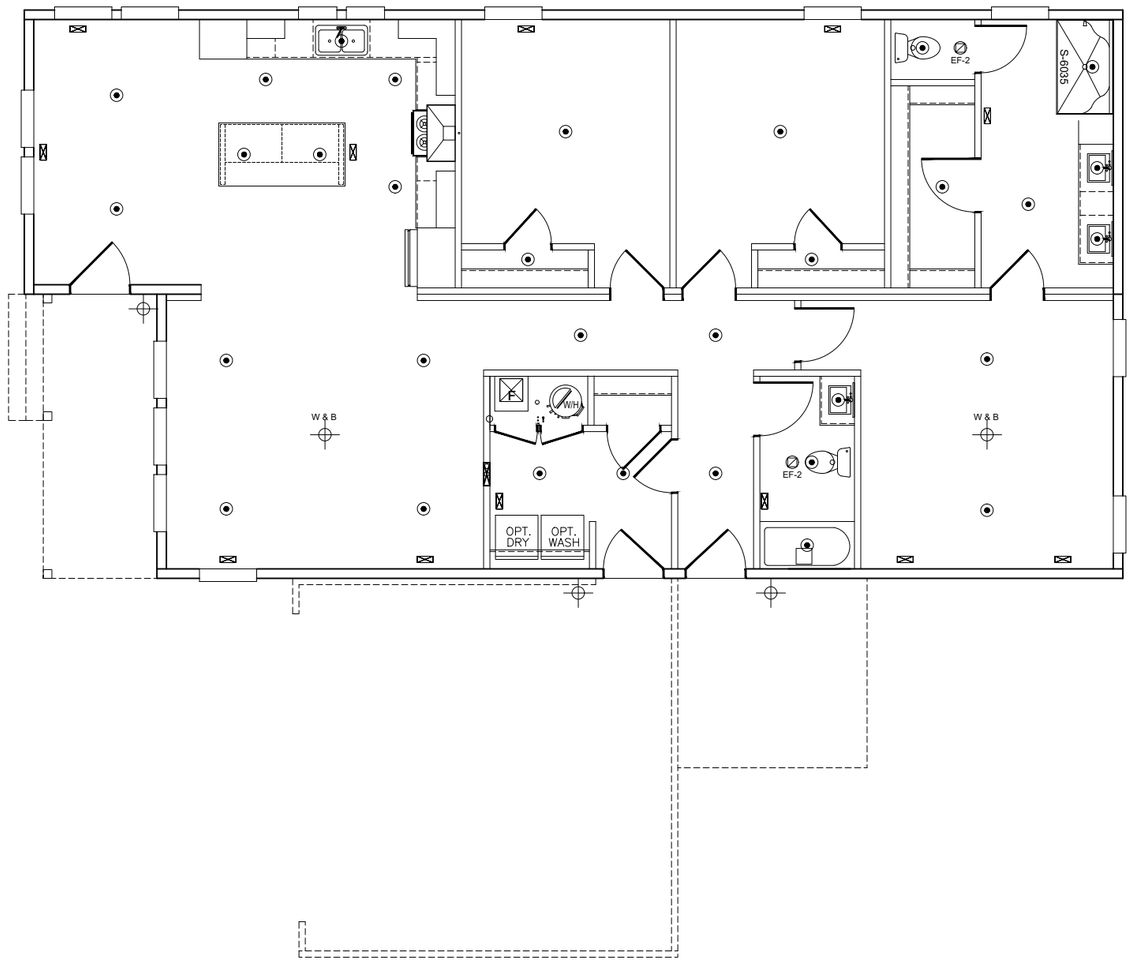

LIGHTING AND FLOOR REGISTER LAYOUT

SYMBOLS LEGEND

W & B	OPT. CEILING FAN or WIRE & BRACE
	WALL OR CEILING MNT FIXTURE
	CAN LIGHT
EF-2	BATH FAN
	HVAC REGISTER
F	HVAC FURNACE
WH	WATER HEATER

NOTES:
1. ALL SYMBOLS MAY NOT BE APPLICABLE TO ALL PROJECTS.

Clayton Built


MODEL NAME: CrossMod_Keeneland_R
MODEL NO.: CrossMod-3258-32-1_Keeneland_R
BOX SIZE: 32' x 58'
MODEL SQ. FT.: 1,635

DATE PRINTED: 9/28/2023
SCALE: 1/8"=1' * UNLESS OTHERWISE NOTED
PLAN NO.: CrossMod-3258-32-1_Keeneland_R
SHEET NAME: ELEC. PLAN
SHEET NO.: A1.1.

File Path:B:\Architecture\CrossMod\DWG Files\3258_KEENELAND\CrossMod-3258-32-1_Keeneland_R.dwg, Last Saved By:Hutsella, Saved Date:9/28/2023 11:20 AM



FRONT ELEVATION

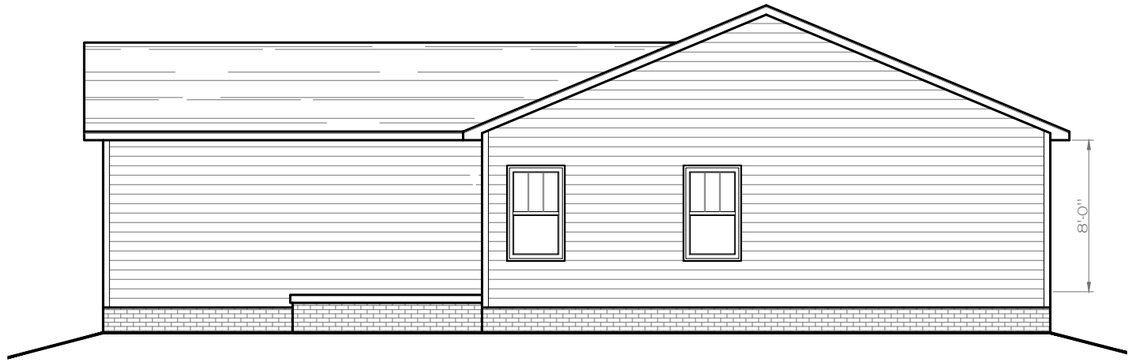

REAR ELEVATION



RIGHT SIDE ELEVATION



LEFT SIDE ELEVATION

Clayton Built

MODEL NAME
CrossMod_Keeneland_R

MODEL NO.
CrossMod-3258-32-1_Keeneland_R

BOX SIZE
32' x 58'

MODEL SQ. FT.
1,635

DATE PRINTED
9/28/2023


SCALE
1/8"=1'
* UNLESS OTHERWISE NOTED

PLAN NO.
CrossMod--3258-32-1_Keeneland_R

SHEET NAME
EXTERIOR ELEVATION

SHEET NO.
A2.0.

File Path:B:\Architecture\CrossMod\DWG Files\3258_KEENELAND\CrossMod--3258-32-1_Keeneland_R.dwg, Last Saved By:Hutsella, Saved Date:9/28/2023 11:20 AM

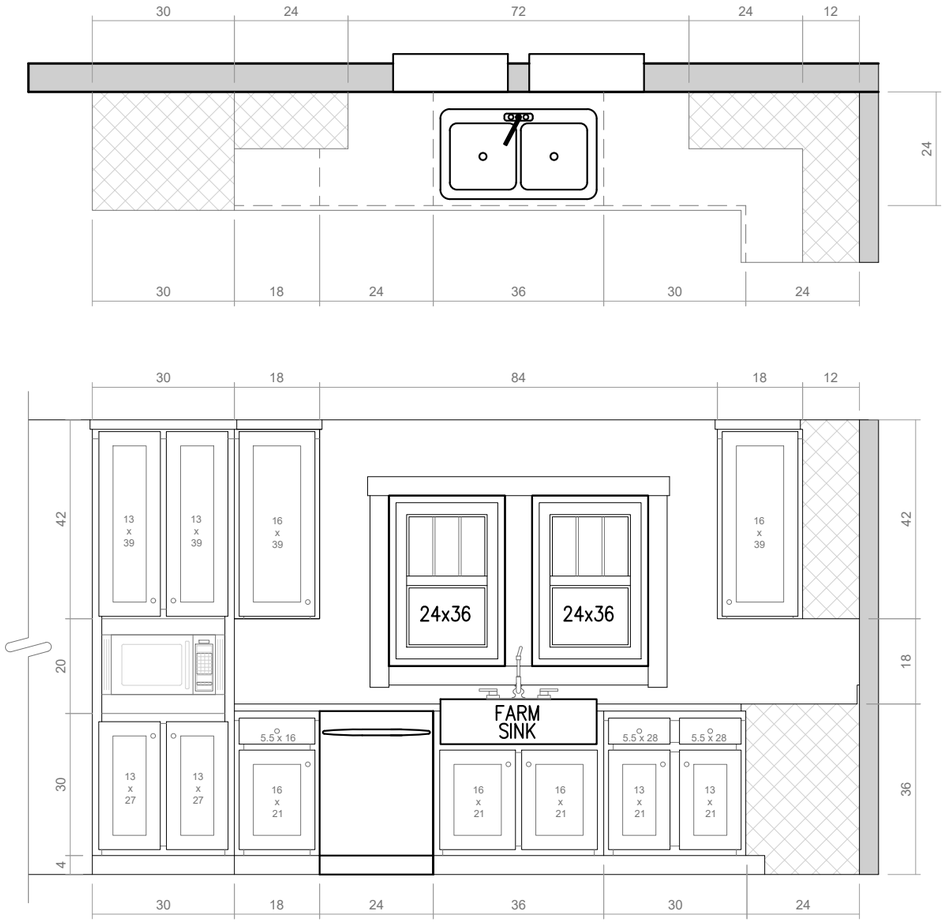

KITCHEN ELEVATION @ SINK / DISHWASHER




KITCHEN ELEVATION @ OVEN / REFRIDGERATOR

Clayton Built


MODEL NAME: CrossMod_Keeneland_R
MODEL NO.: CrossMod-3258-32-1_Keeneland_R
BOX SIZE: 32' x 58'
MODEL SQ. FT.: 1,635

DATE PRINTED: 9/28/2023
SCALE: 3/8"=1'
* UNLESS OTHERWISE NOTED
PLAN NO.: CrossMod-3258-32-1_Keeneland_R
SHEET NAME: CABINETS KITCHEN
SHEET NO.: A3.0.

File Path:B:\Architecture\CrossMod\DWG Files\3258_KEENELAND\CrossMod--3258-32-1_Keeneland_R.dwg, Last Saved By:Hutsella, Saved Date:9/28/2023 11:20 AM

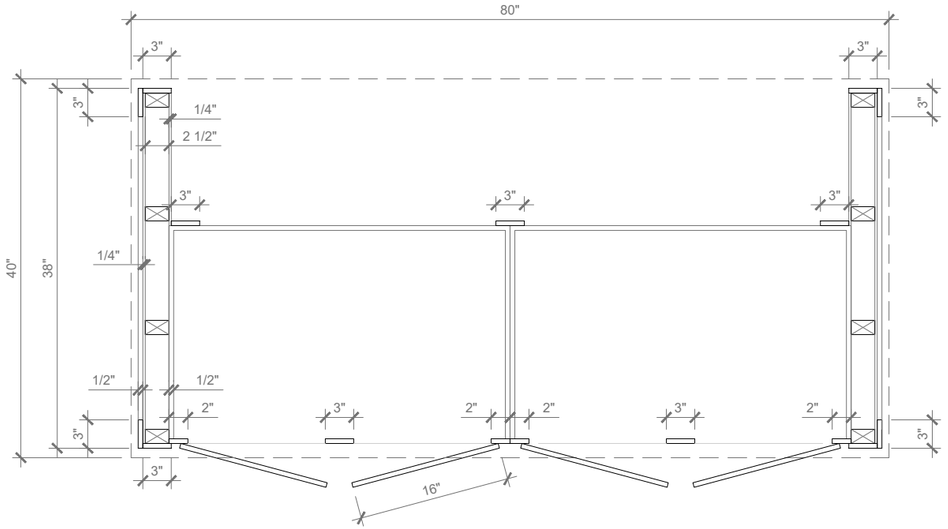

ISLAND PLAN/SECTION
$\frac{3}{4}$" = 1'-0"

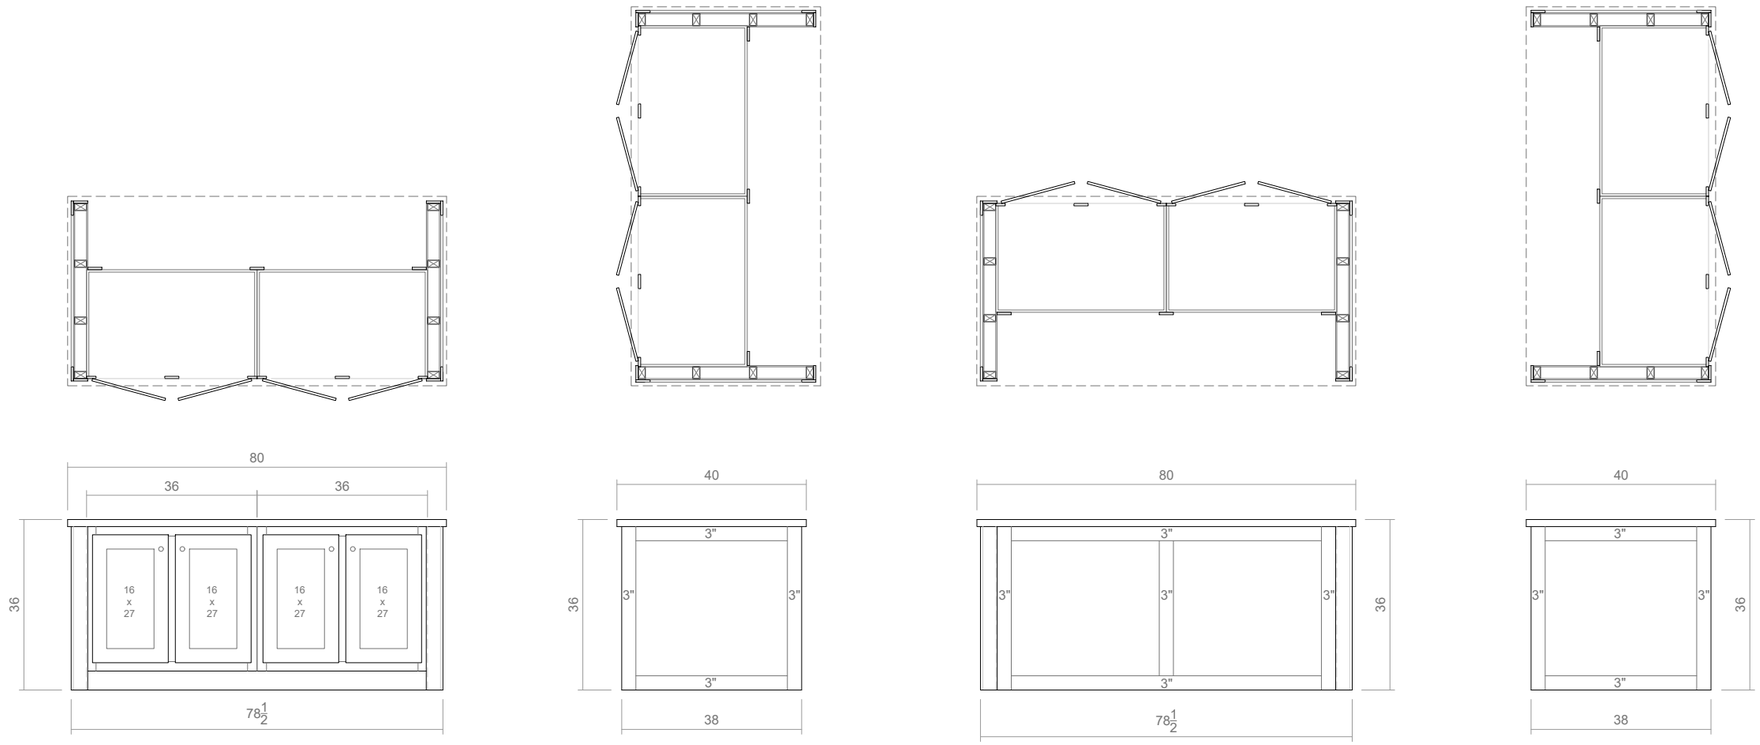


ISLAND ELEVATIONS
$\frac{3}{8}$" = 1'-0"

Clayton Built


MODEL NAME: CrossMod_Keeneland_R
MODEL NO.: CrossMod-3258-32-1_Keeneland_R
BOX SIZE: 32' x 58'
MODEL SQ. FT.: 1,635

DATE PRINTED: 9/28/2023
SCALE: VARIES
* UNLESS OTHERWISE NOTED
PLAN NO.: CrossMod--3258-32-1_Keeneland_R
SHEET NAME: CABINETS KITCHEN
SHEET NO.: A3.1.

File Path:B:\Architecture\CrossMod\DWG Files\3258_KEENELAND\CrossMod--3258-32-1_Keeneland_R.dwg, Last Saved By:Hutsella, Saved Date:9/28/2023 11:20 AM

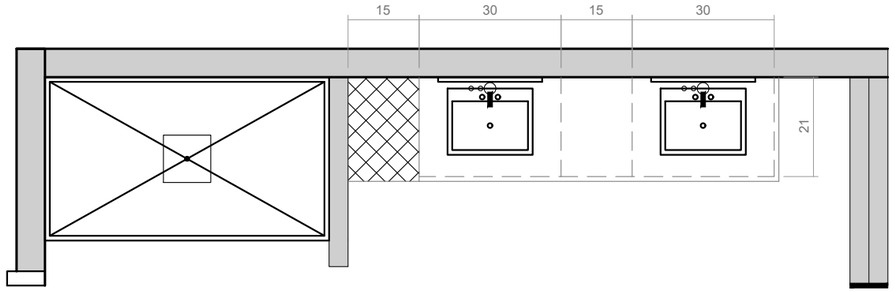

PRIMARY BATH
VANITY ELEVATION

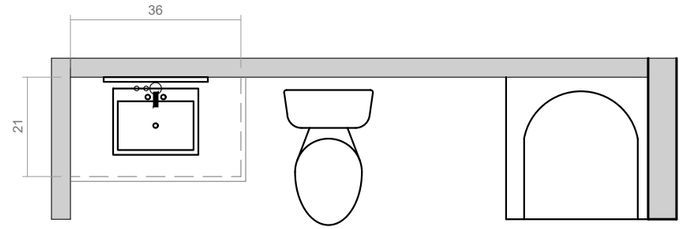


HALL BATHROOM
VANITY ELEVATION

Clayton Built

MODEL NAME: CrossMod_Keeneland_R
MODEL NO.: CrossMod-3258-32-1_Keeneland_R
BOX SIZE: 32' x 58'
MODEL SQ. FT.: 1,635


DATE PRINTED: 9/28/2023
SCALE: 3/8"=1'
* UNLESS OTHERWISE NOTED
PLAN NO.: CrossMod--3258-32-1_Keeneland_R
SHEET NAME: CABINETS BATH
SHEET NO.: A3.2


File Path:B:\Architecture\CrossMod\DWG Files\3258_KEENELAND\CrossMod--3258-32-1_Keeneland_R.dwg, Last Saved By:Hulsella, Saved Date:9/28/2023 11:20 AM

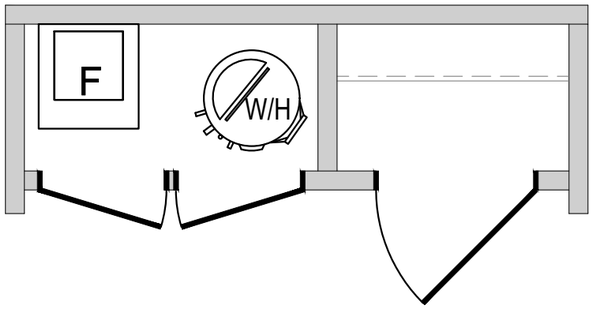




INTERIOR ELEVATION @
UTILITY CLOSET

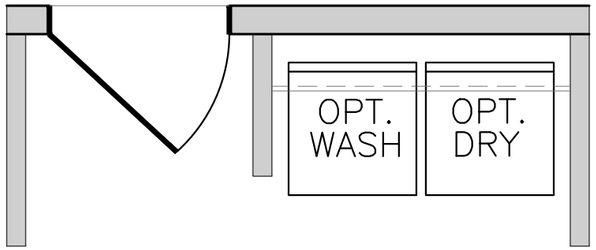

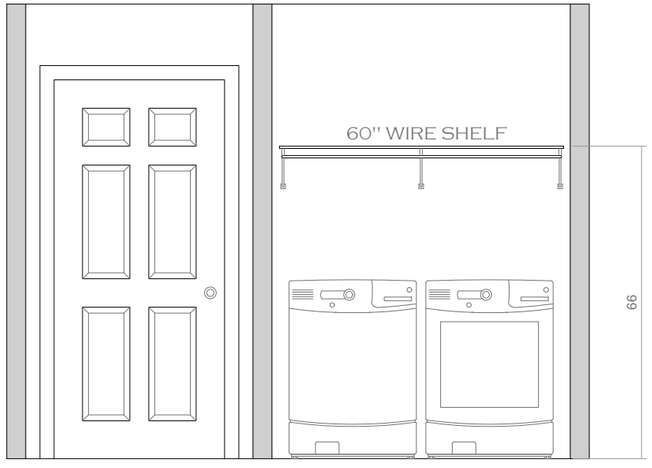

INTERIOR ELEVATION @
WASHER / DRYER

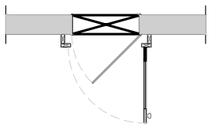


PROPOSED CABINET DOOR
COVER @ PANEL BOX
(NEEDS TO BE PROTOTYPED)

Clayton Built

MODEL NAME: CrossMod_Keeneland_R
MODEL NO.: CrossMod-3258-32-1_Keeneland_R
BOX SIZE: 32' x 58'
MODEL SQ. FT.: 1,635

DATE PRINTED: 9/28/2023
SCALE: 3/8"=1'
* UNLESS OTHERWISE NOTED
PLAN NO.: CrossMod-3258-32-1_Keeneland_R
SHEET NAME: MISC. DETAILS
SHEET NO.: A3.3.

File Path:B:\Architecture\CrossMod\DWG Files\3258_KEENELAND\CrossMod--3258-32-1_Keeneland_R.dwg, Last Saved By:Hulsella, Saved Date:9/28/2023 11:20 AM

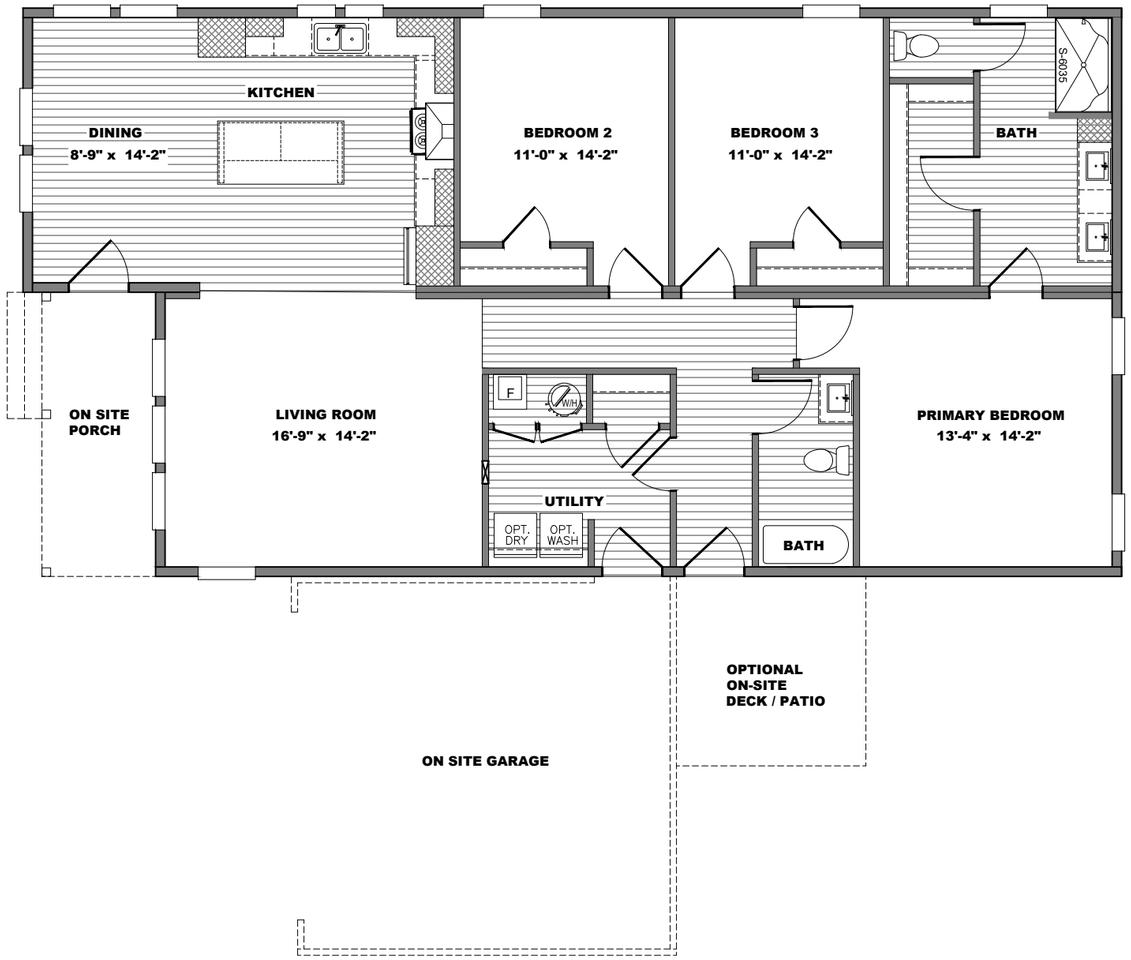

Clayton Built

MODEL NAME: CrossMod_Keeneland_R

MODEL NO.: CrossMod-3258-32-1_Keeneland_R

BOX SIZE: 32' x 58'

MODEL SQ. FT.: 1,635

DATE PRINTED: 9/28/2023

SCALE: 1/8"=1'
* UNLESS OTHERWISE NOTED


PLAN NO.: CrossMod--3258-32-1_Keeneland_R

SHEET NAME: SALESLIT

SHEET NO.: A4.0.

File Path:B:\Architecture\CrossMod\DWG Files\3258_KEENELAND\CrossMod--3258-32-1_Keeneland_R.dwg, Last Saved By:Hutsella, Saved Date:9/28/2023 11:20 AM

"CrossMod_Keeneland_R"

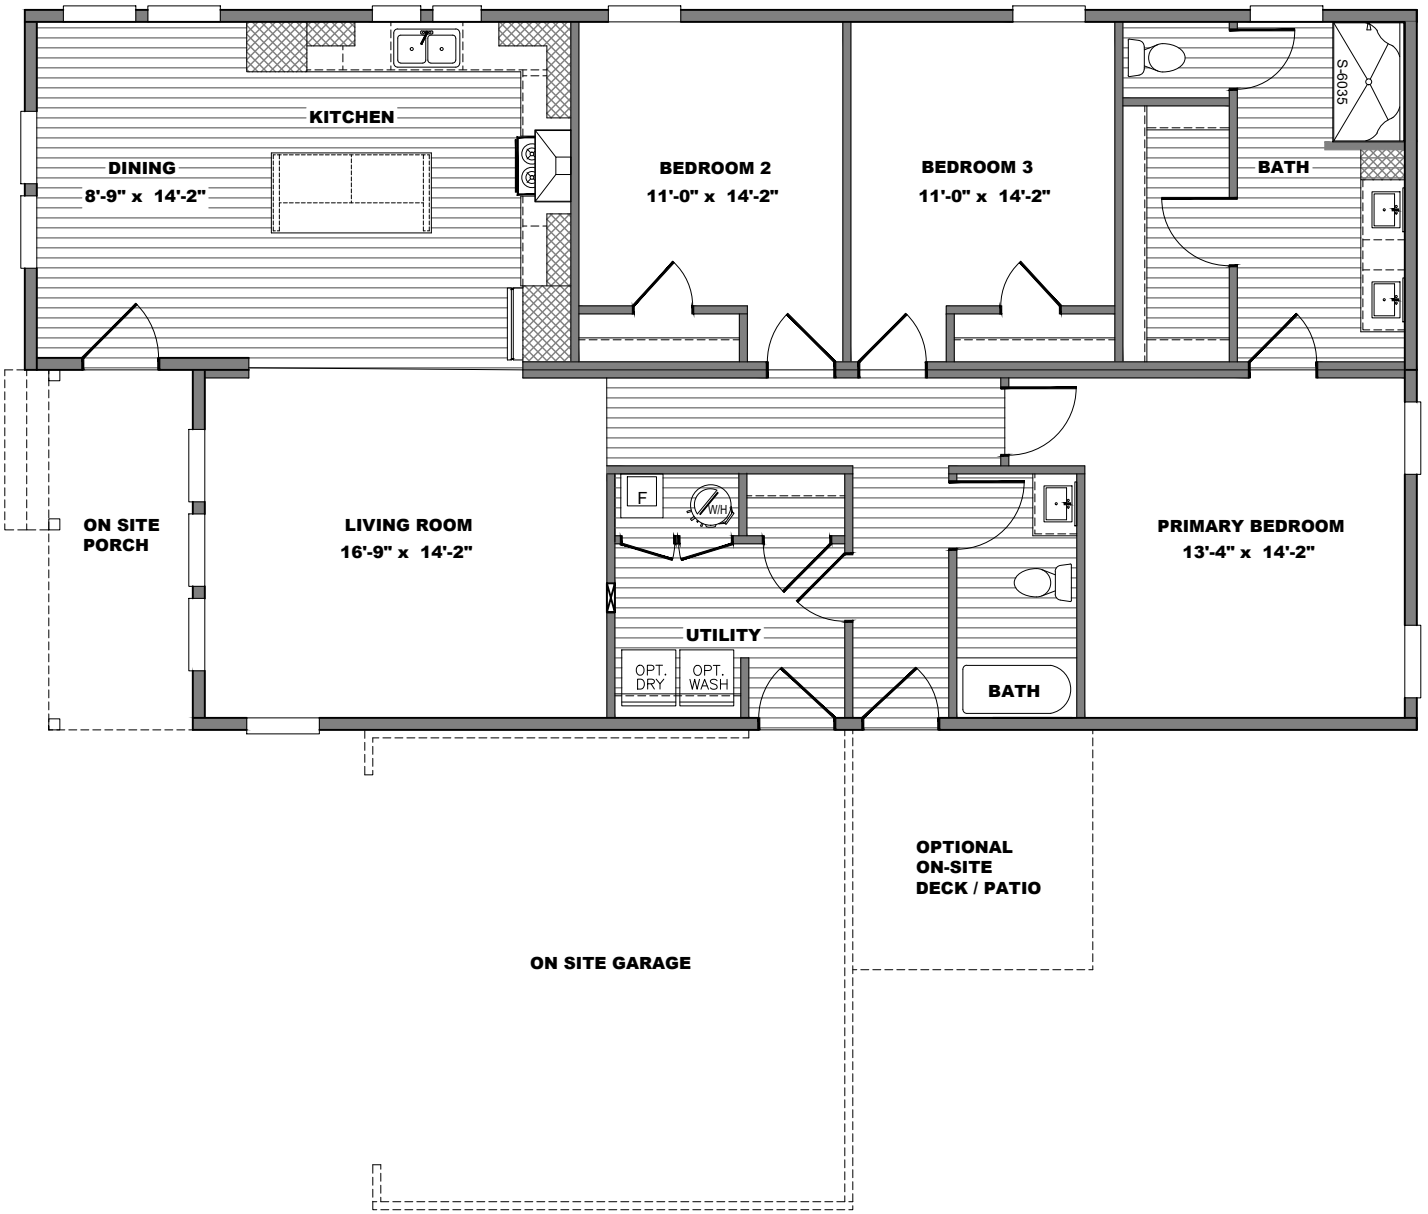

MODEL #CrossMod-3258-32-1_Keeneland_R SQ.FT. 1,635 DRAWING # CROSSMOD-3258-32-1_KEENELAND_R

File Path:B:\Architecture\CrossMod\DWG Files\3258_KEENELAND\CrossMod--3258-32-1_Keeneland_R.dwg, Last Saved By:Hutsella, Saved Date:9/28/2023 11:20 AM, Date Printed:9/28/23 11:51 AM