

INDEX

A0.0	COVER SHEET
A1.0	FLOOR PLAN
A1.1	LIGHTING AND FLOOR REGISTER LAYOUT
A2.0	ELEVATIONS - STANDARD
A2.1	ELEVATIONS - OPTIONS
A3.0	INTERIOR DETAILS - KITCHEN
A3.1	INTERIOR DETAILS - KITCHEN
A3.2	INTERIOR DETAILS - BATHS
A3.3	INTERIOR DETAILS - MISC
A4.0	SALESLIT PRINT
	SALESLIT
	SALESLIT (2)
	SALESLIT (3)
	SALESLIT (4)

GENERAL NOTES

1. THIS PACKAGE IS INTENDED TO RELAY DESIGN INTENT AND IS NOT FOR CONSTRUCTION.
2. PLEASE CONTACT ANDY HUTSELL AT ANDY.HUTSELL@CLAYTONHOMES.COM WITH QUESTIONS REGARDING THESE DRAWINGS.

SYMBOLS AND ABBREVIATIONS


CLG	CEILING
DR	DOOR
EF	EXHAUST FAN
FLR	FLOOR
MNT	MOUNT
OPT	OPTIONAL
RAG	RETURN AIR GRILLE
SEP	STANDARD ELECTRIC PANEL
SGD	SLIDING GLASS DOOR

Clayton Built


MODEL NAME: CrossMod_Magnolia_R
MODEL NO.: CrossMod-3258-32-2_Magnolia_R
BOX SIZE: 32' x 58'
MODEL SQ. FT.: 1,635

DATE PRINTED: 9/28/2023
SCALE: N.T.S. (*UNLESS OTHERWISE NOTED)
PLAN NO.: CrossMod--3258-32-2_Magnolia_R
SHEET NAME: COVER SHEET
SHEET NO.: A0.0.


File Path:B:\Architecture\CrossMod\DWG Files\3258_MAGNOLIA\CrossMod--3258-32-2_Magnolia_R.dwg, Last Saved By:Hutsella, Saved Date:9/28/2023 11:27 AM

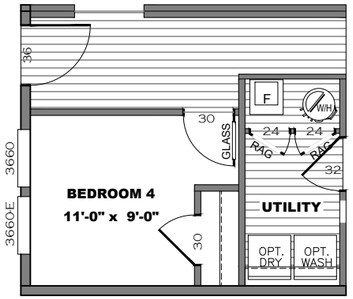


FOURTH BEDROOM OPTION

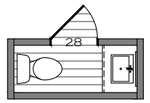

HALF BATH OPTION

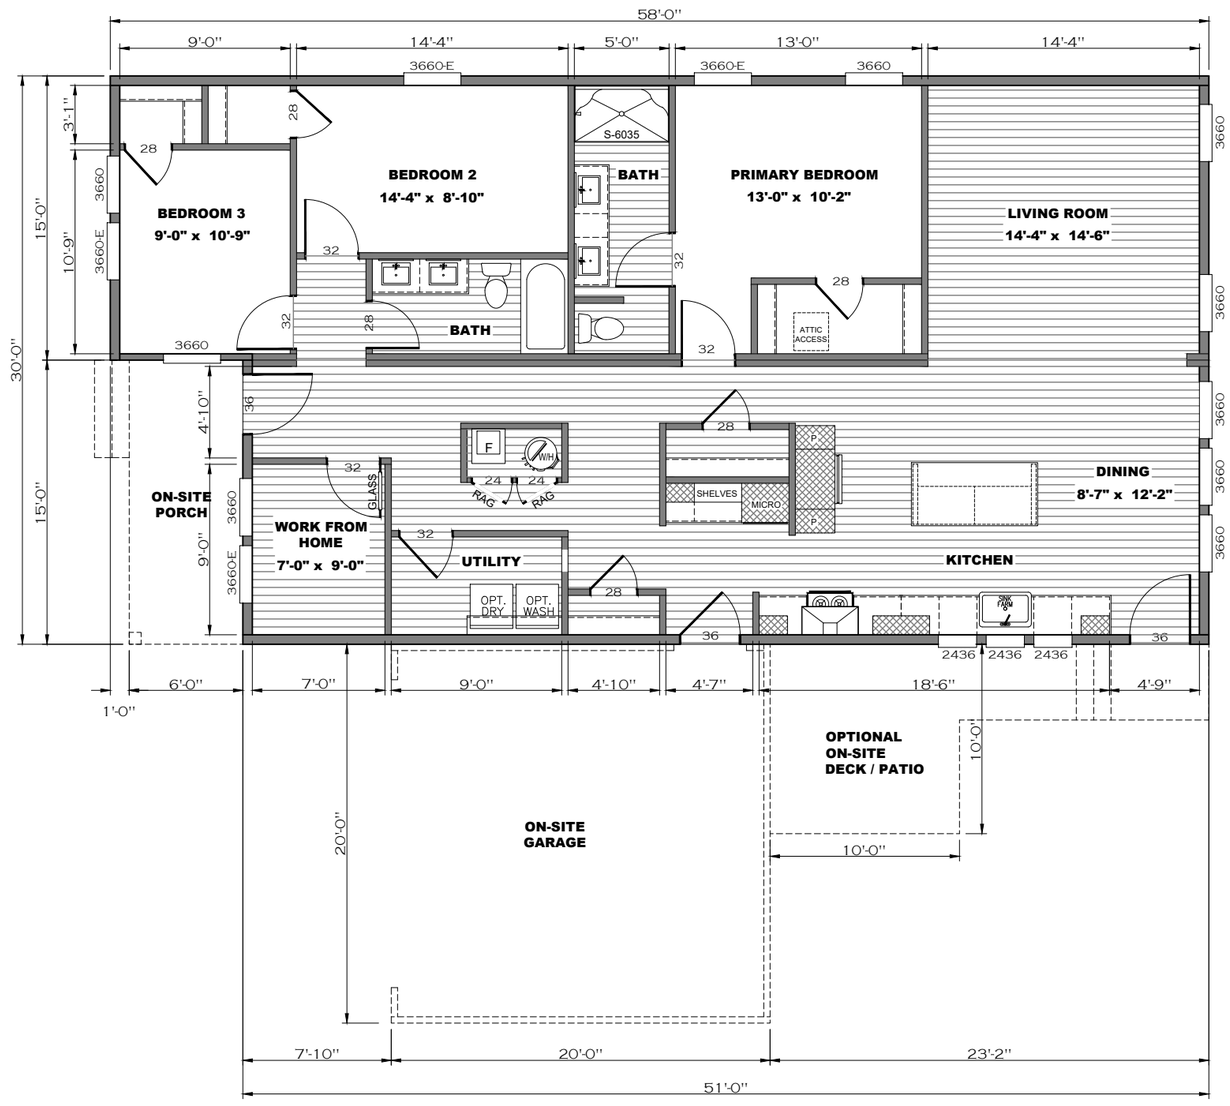

FLOOR PLAN

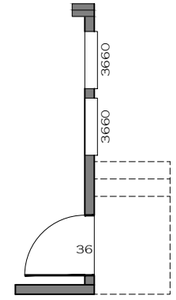

Clayton Built

MODEL NAME: CrossMod_Magnolia_R
MODEL NO.: CrossMod-3258-32-2_Magnolia_R
BOX SIZE: 32' x 58'
MODEL SQ. FT.: 1,635

DATE PRINTED: 9/28/2023


SCALE: 1/8"=1'
* UNLESS OTHERWISE NOTED

PLAN NO.: CrossMod--3258-32-2_Magnolia_R

SHEET NAME: FLOOR PLAN

SHEET NO.: A1.0.

File Path:B:\Architecture\CrossMod\DWG Files\3258_MAGNOLIA\CrossMod--3258-32-2_Magnolia_R.dwg, Last Saved By:Hutsella, Saved Date:9/28/2023 11:27 AM

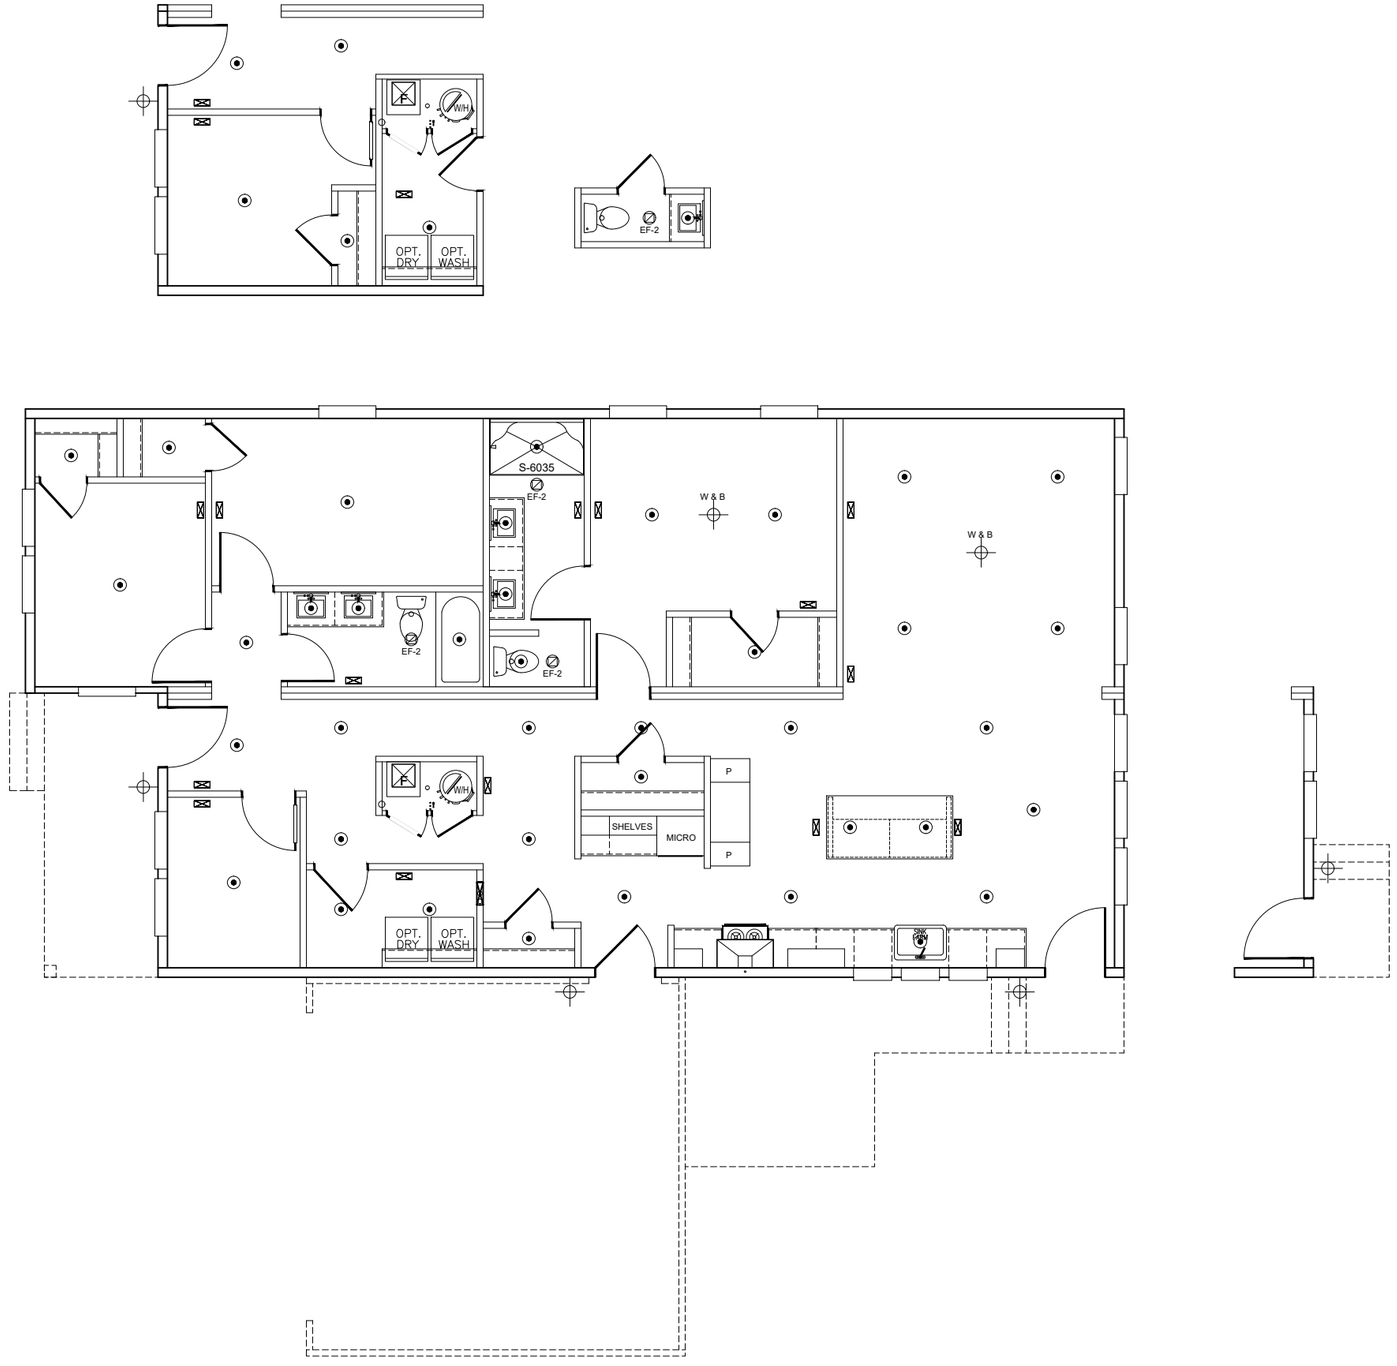

LIGHTING AND FLOOR REGISTER LAYOUT

SYMBOLS LEGEND	
W & B	OPT. CEILING FAN or WIRE & BRACE
	WALL OR CEILING MNT FIXTURE
	CAN LIGHT
EF-2	BATH FAN
	HVAC REGISTER
F	HVAC FURNACE
W/H	WATER HEATER


NOTES:
1. ALL SYMBOLS MAY NOT BE APPLICABLE TO ALL PROJECTS.

Clayton Built

MODEL NAME: CrossMod_Magnolia_R
MODEL NO.: CrossMod-3258-32-2_Magnolia_R
BOX SIZE: 32' x 58'
MODEL SQ. FT.: 1,635

DATE PRINTED: 9/28/2023
SCALE: 1/8"=1'
* UNLESS OTHERWISE NOTED
PLAN NO.: CrossMod-3258-32-2_Magnolia_R
SHEET NAME: ELEC. PLAN
SHEET NO.: A1.1.


File Path:B:\Architecture\CrossMod\DWG Files\3258_MAGNOLIA\CrossMod--3258-32-2_Magnolia_R.dwg, Last Saved By:Hutsella, Saved Date:9/28/2023 11:27 AM

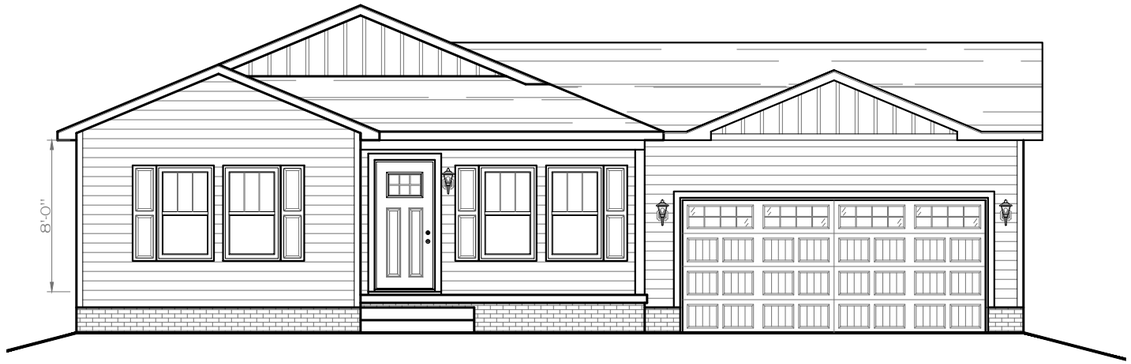

FRONT ELEVATION



REAR ELEVATION

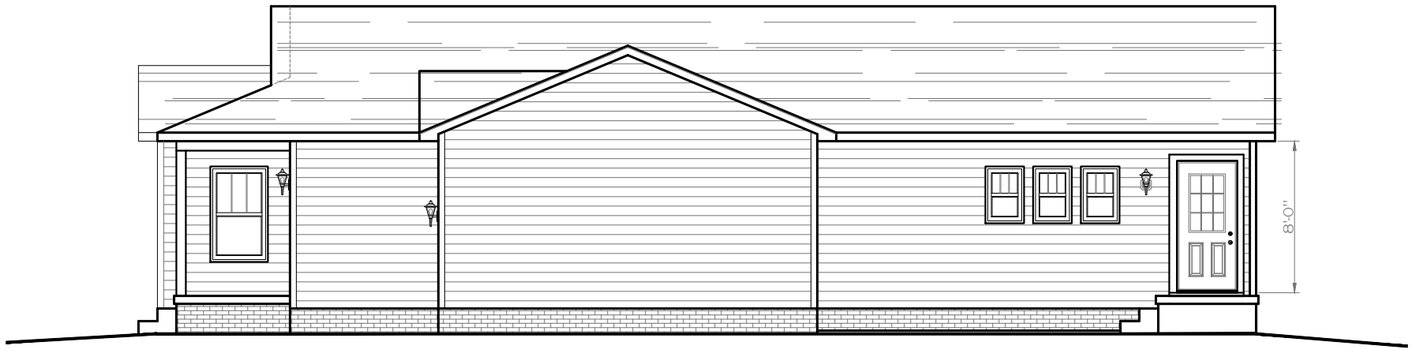

RIGHT SIDE ELEVATION



LEFT SIDE ELEVATION

Clayton Built

MODEL NAME
CrossMod_Magnolia_R

MODEL NO.
CrossMod-3258-32-2_Magnolia_R

BOX SIZE
32' x 58'

MODEL SQ. FT.
1,635

DATE PRINTED
9/28/2023

SCALE
1/8"=1'
* UNLESS OTHERWISE NOTED

PLAN NO.
CrossMod-3258-32-2_Magnolia_R


SHEET NAME
EXTERIOR ELEVATION

SHEET NO.
A2.0.

File Path:B:\Architecture\CrossMod\DWG Files\3258_MAGNOLIA\CrossMod--3258-32-2_Magnolia_R.dwg, Last Saved By:Hutsella, Saved Date:9/28/2023 11:27 AM



REAR ELEVATION FOR
ALTERNATE BACK DOOR OPTION

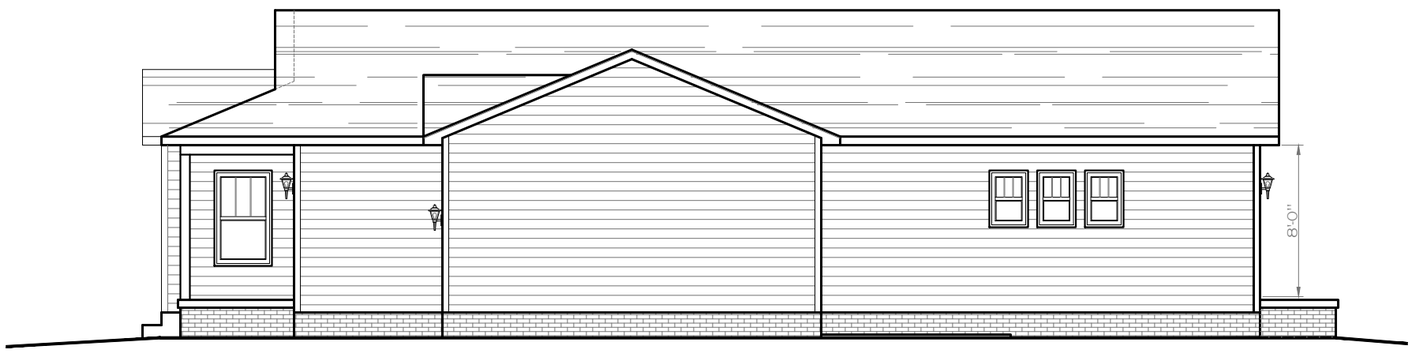

RIGHT SIDE ELEVATION FOR
ALTERNATE BACK DOOR OPTION

Clayton Built

MODEL NAME
CrossMod_Magnolia_R

MODEL NO.
CrossMod-3258-32-2_Magnolia_R

BOX SIZE
32' x 58'

MODEL SQ. FT.
1,635

DATE PRINTED
9/28/2023

SCALE
1/8"=1'
* UNLESS OTHERWISE NOTED

PLAN NO.
CrossMod-3258-32-2_Magnolia_R


SHEET NAME
EXTERIOR ELEVATION

SHEET NO.
A2.1.


File Path:B:\Architecture\CrossMod\DWG Files\3258_MAGNOLIA\CrossMod-3258-32-2_Magnolia_R.dwg, Last Saved By:Hutsella, Saved Date:9/28/2023 11:27 AM



KITCHEN ELEVATION @ SINK / OVEN WALL

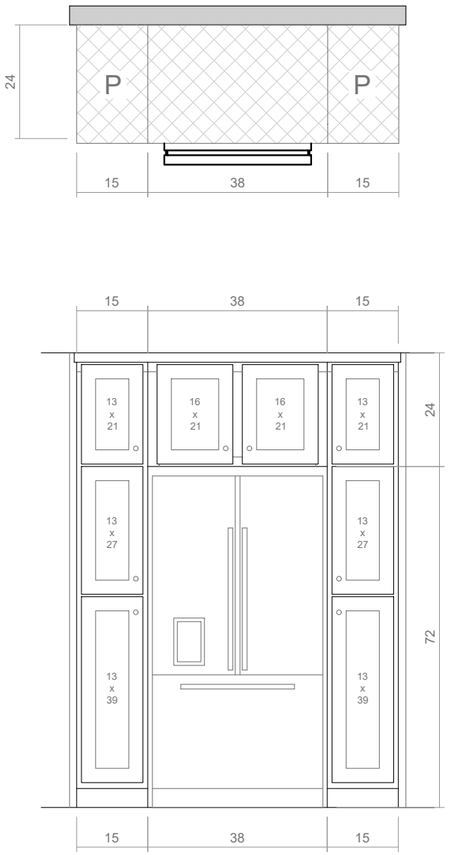

KITCHEN ELEVATION @ REFRIDGERATOR

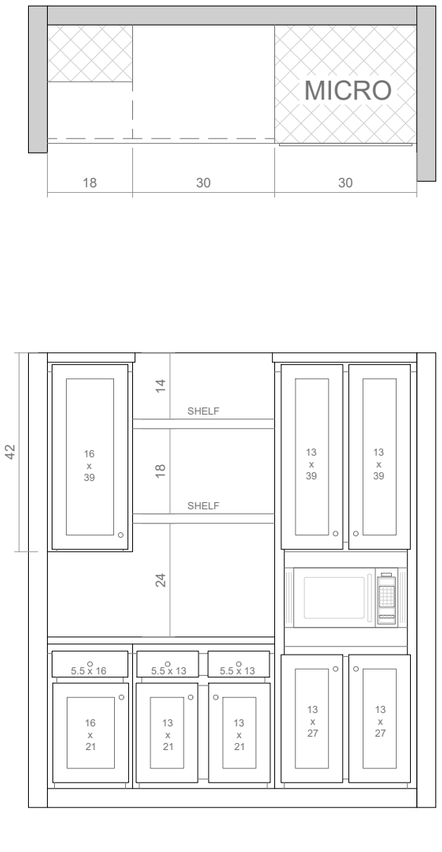

KITCHEN ELEVATION @ COFFEE BAR / MICROWAVE

Clayton Built

MODEL NAME: CrossMod_Magnolia_R

MODEL NO.: CrossMod-3258-32-2_Magnolia_R

BOX SIZE: 32' x 58'

MODEL SQ. FT.: 1,635

DATE PRINTED: 9/28/2023


SCALE: 3/8"=1'
* UNLESS OTHERWISE NOTED

PLAN NO.: CrossMod--3258-32-2_Magnolia_R


SHEET NAME: CABINETS KITCHEN

SHEET NO.: A3.0.

File Path:B:\Architecture\CrossMod\DWG Files\3258_MAGNOLIA\CrossMod--3258-32-2_Magnolia_R.dwg, Last Saved By:Hutsella, Saved Date:9/28/2023 11:27 AM

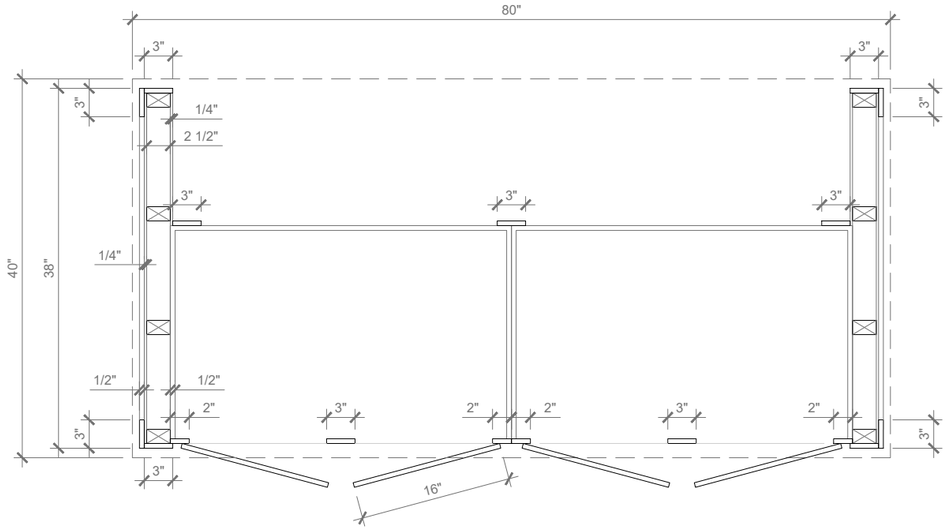


ISLAND PLAN/SECTION
$\frac{3}{4}$" = 1'-0"

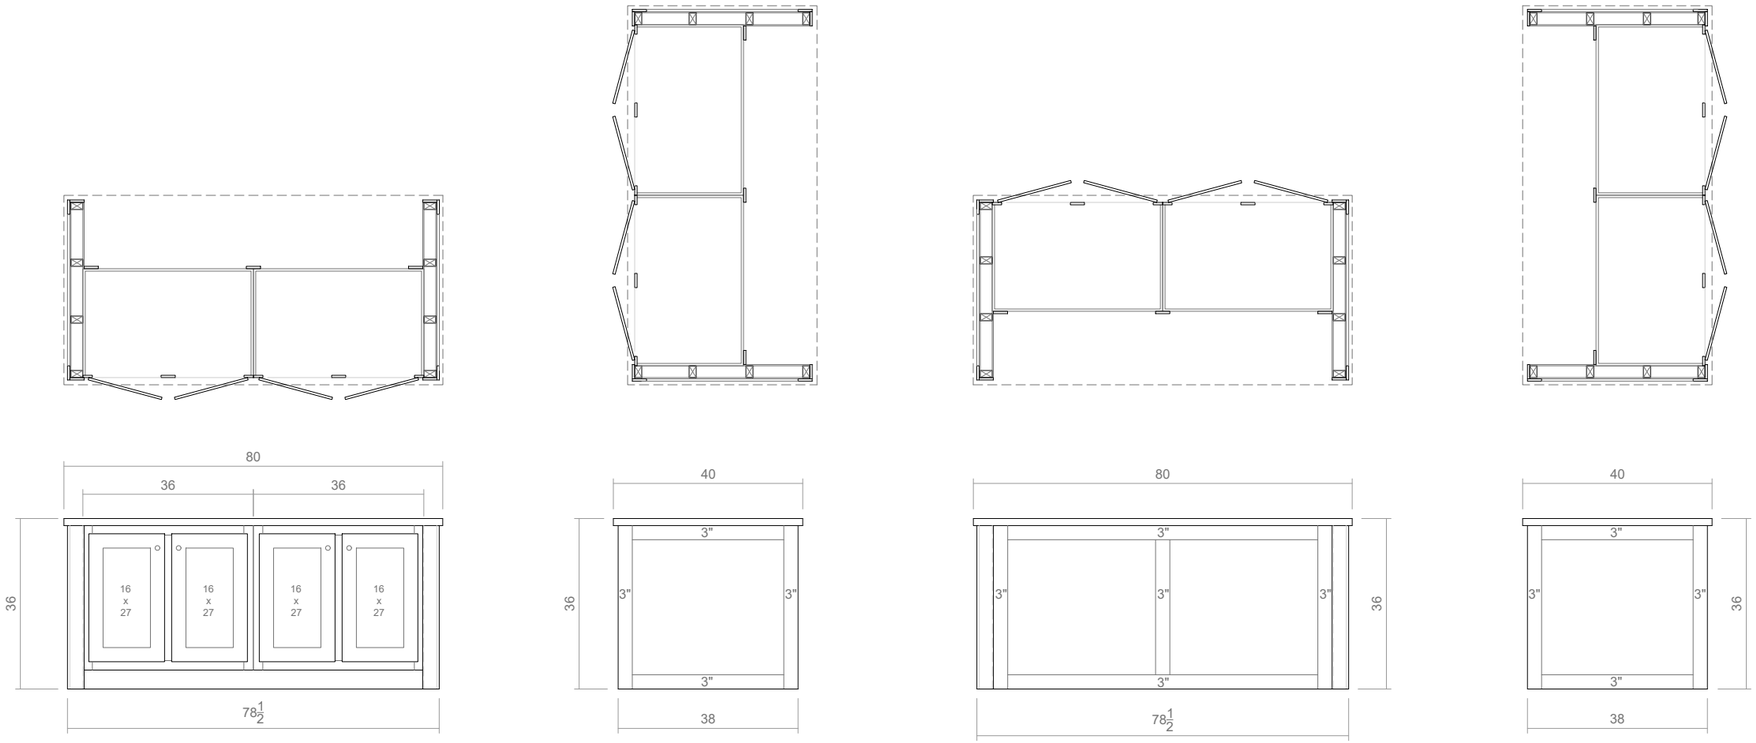


ISLAND ELEVATIONS
$\frac{3}{8}$" = 1'-0"


MODEL NAME
CrossMod_Magnolia_R
MODEL NO.
CrossMod-3258-32-2_Magnolia_R
BOX SIZE
32' x 58'
MODEL SQ. FT.
1,635
DATE PRINTED
9/28/2023
SCALE
VARIES
* UNLESS OTHERWISE NOTED
PLAN NO.
CrossMod--3258-32-2_Magnolia_R
SHEET NAME
CABINETS
KITCHEN
SHEET NO.
A3.1.
File Path:B:\Architecture\CrossMod\DWG Files\3258_MAGNOLIA\CrossMod--3258-32-2_Magnolia_R.dwg, Last Saved By:Hutsella, Saved Date:9/28/2023 11:27 AM

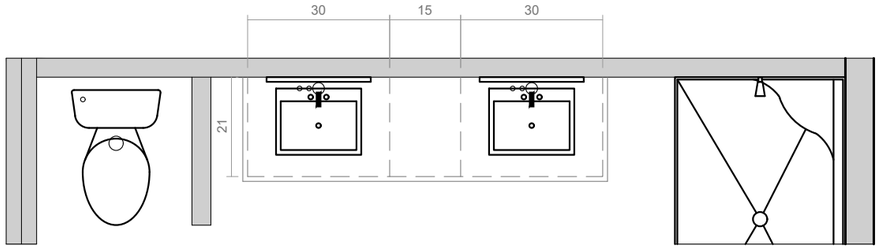





PRIMARY BATH
VANITY ELEVATION

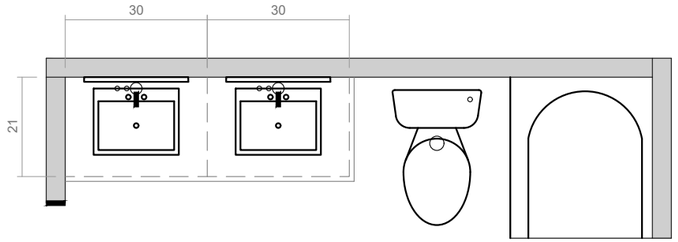

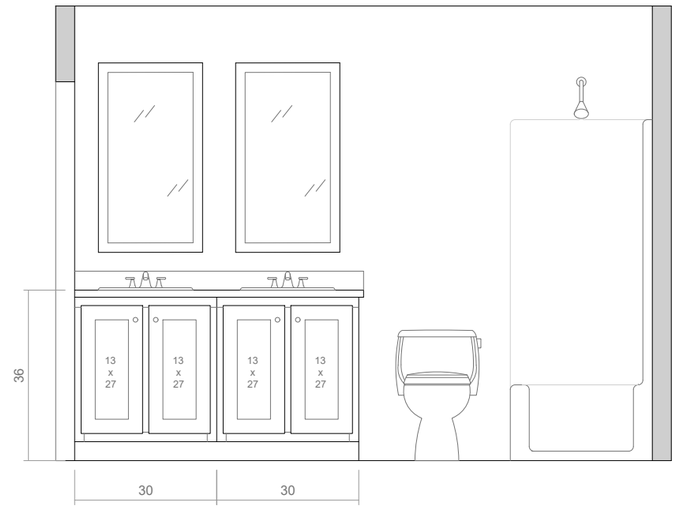

HALL BATHROOM
VANITY ELEVATION

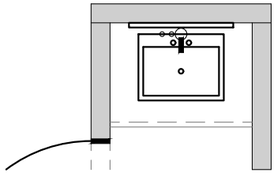

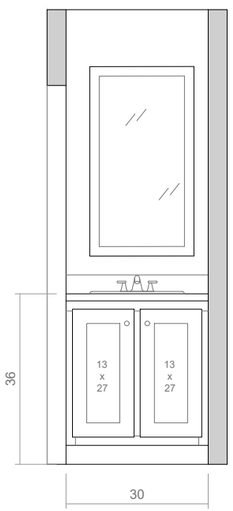


HALF BATH
VANITY ELEVATION


Clayton Built

MODEL NAME: CrossMod_Magnolia_R
MODEL NO.: CrossMod-3258-32-2_Magnolia_R
BOX SIZE: 32' x 58'
MODEL SQ. FT.: 1,635


DATE PRINTED: 9/28/2023
SCALE: 3/8"=1' * UNLESS OTHERWISE NOTED
PLAN NO.: CrossMod--3258-32-2_Magnolia_R
SHEET NAME: CABINETS BATH
SHEET NO.: A3.2


File Path:B:\Architecture\CrossMod\DWG Files\3258_MAGNOLIA\CrossMod--3258-32-2_Magnolia_R.dwg, Last Saved By:Hutsella, Saved Date:9/28/2023 11:27 AM

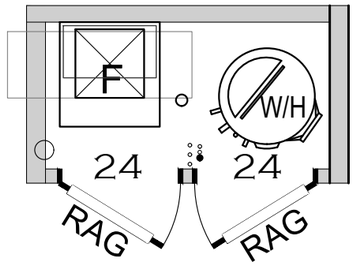

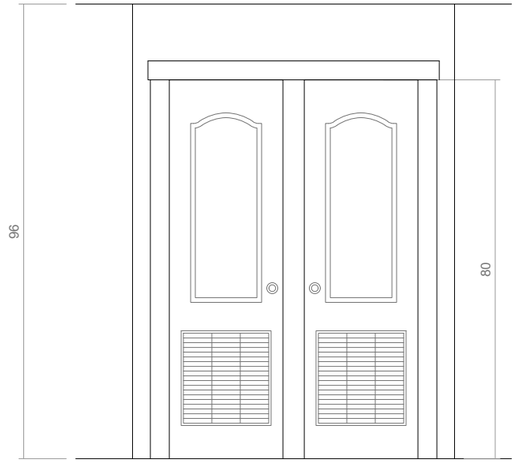



INTERIOR ELEVATION @ UTILITY CLOSET

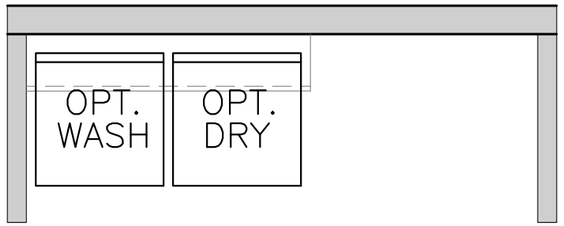

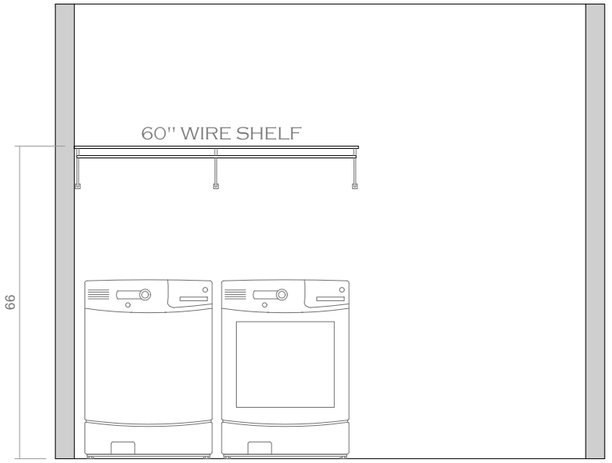

INTERIOR ELEVATION @ WASHER / DRYER

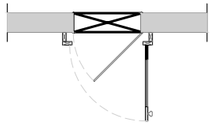

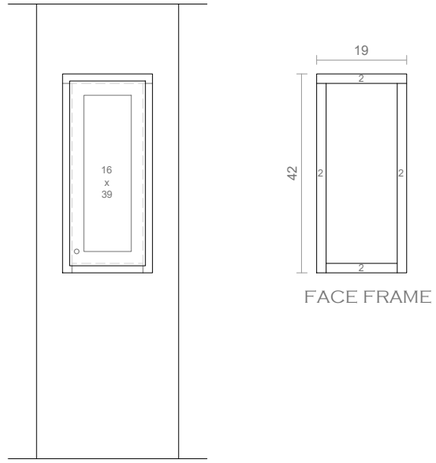


PROPOSED CABINET DOOR COVER @ PANEL BOX (NEEDS TO BE PROTOTYPED)

Clayton Built


MODEL NAME: CrossMod_Magnolia_R
MODEL NO.: CrossMod-3258-32-2_Magnolia_R
BOX SIZE: 32' x 58'
MODEL SQ. FT.: 1,635

DATE PRINTED: 9/28/2023
SCALE: 3/8"=1' * UNLESS OTHERWISE NOTED
PLAN NO.: CrossMod--3258-32-2_Magnolia_R
SHEET NAME: MISC. DETAILS
SHEET NO.: A3.3.


File Path:B:\Architecture\CrossMod\DWG Files\3258_MAGNOLIA\CrossMod--3258-32-2_Magnolia_R.dwg, Last Saved By:Hutsella, Saved Date:9/28/2023 11:27 AM

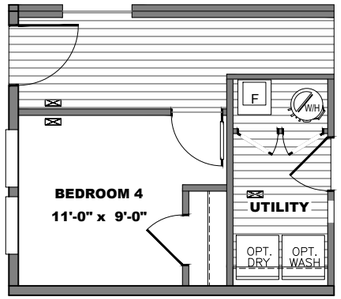


FOURTH BEDROOM OPTION

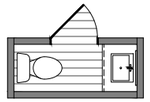

HALF BATH OPTION

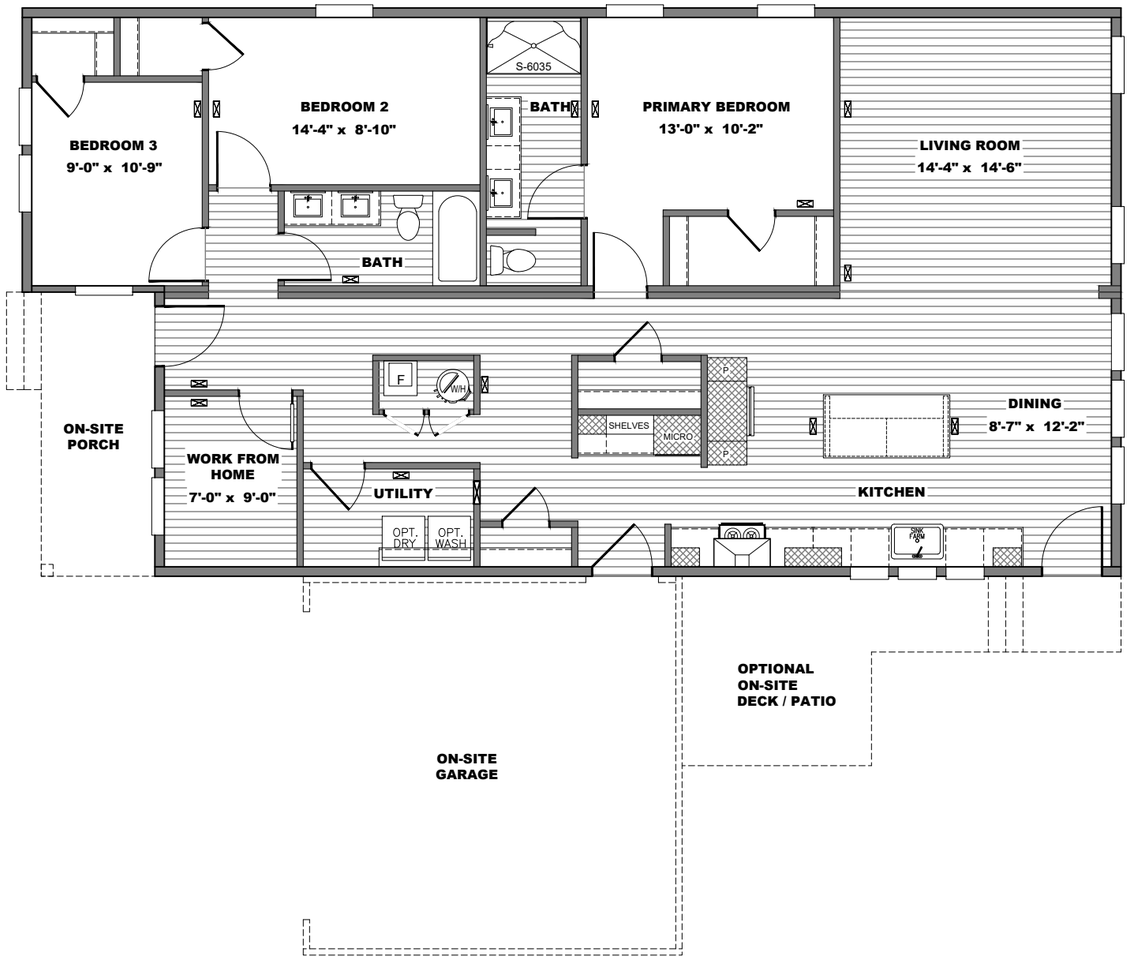

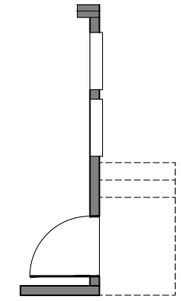

Clayton Built

MODEL NAME
CrossMod_Magnolia_R

MODEL NO.
CrossMod-3258-32-2_Magnolia_R

BOX SIZE
32' x 58'

MODEL SQ. FT.
1,635

DATE PRINTED
9/28/2023

SCALE
1/8"=1'
* UNLESS OTHERWISE NOTED


PLAN NO.
CrossMod--3258-32-2_Magnolia_R

SHEET NAME
SALESLIT

SHEET NO.
A4.0.

File Path:B:\Architecture\CrossMod\DWG Files\3258_MAGNOLIA\CrossMod--3258-32-2_Magnolia_R.dwg, Last Saved By:Hutsella, Saved Date:9/28/2023 11:27 AM


"CrossMod_Magnolia_R"

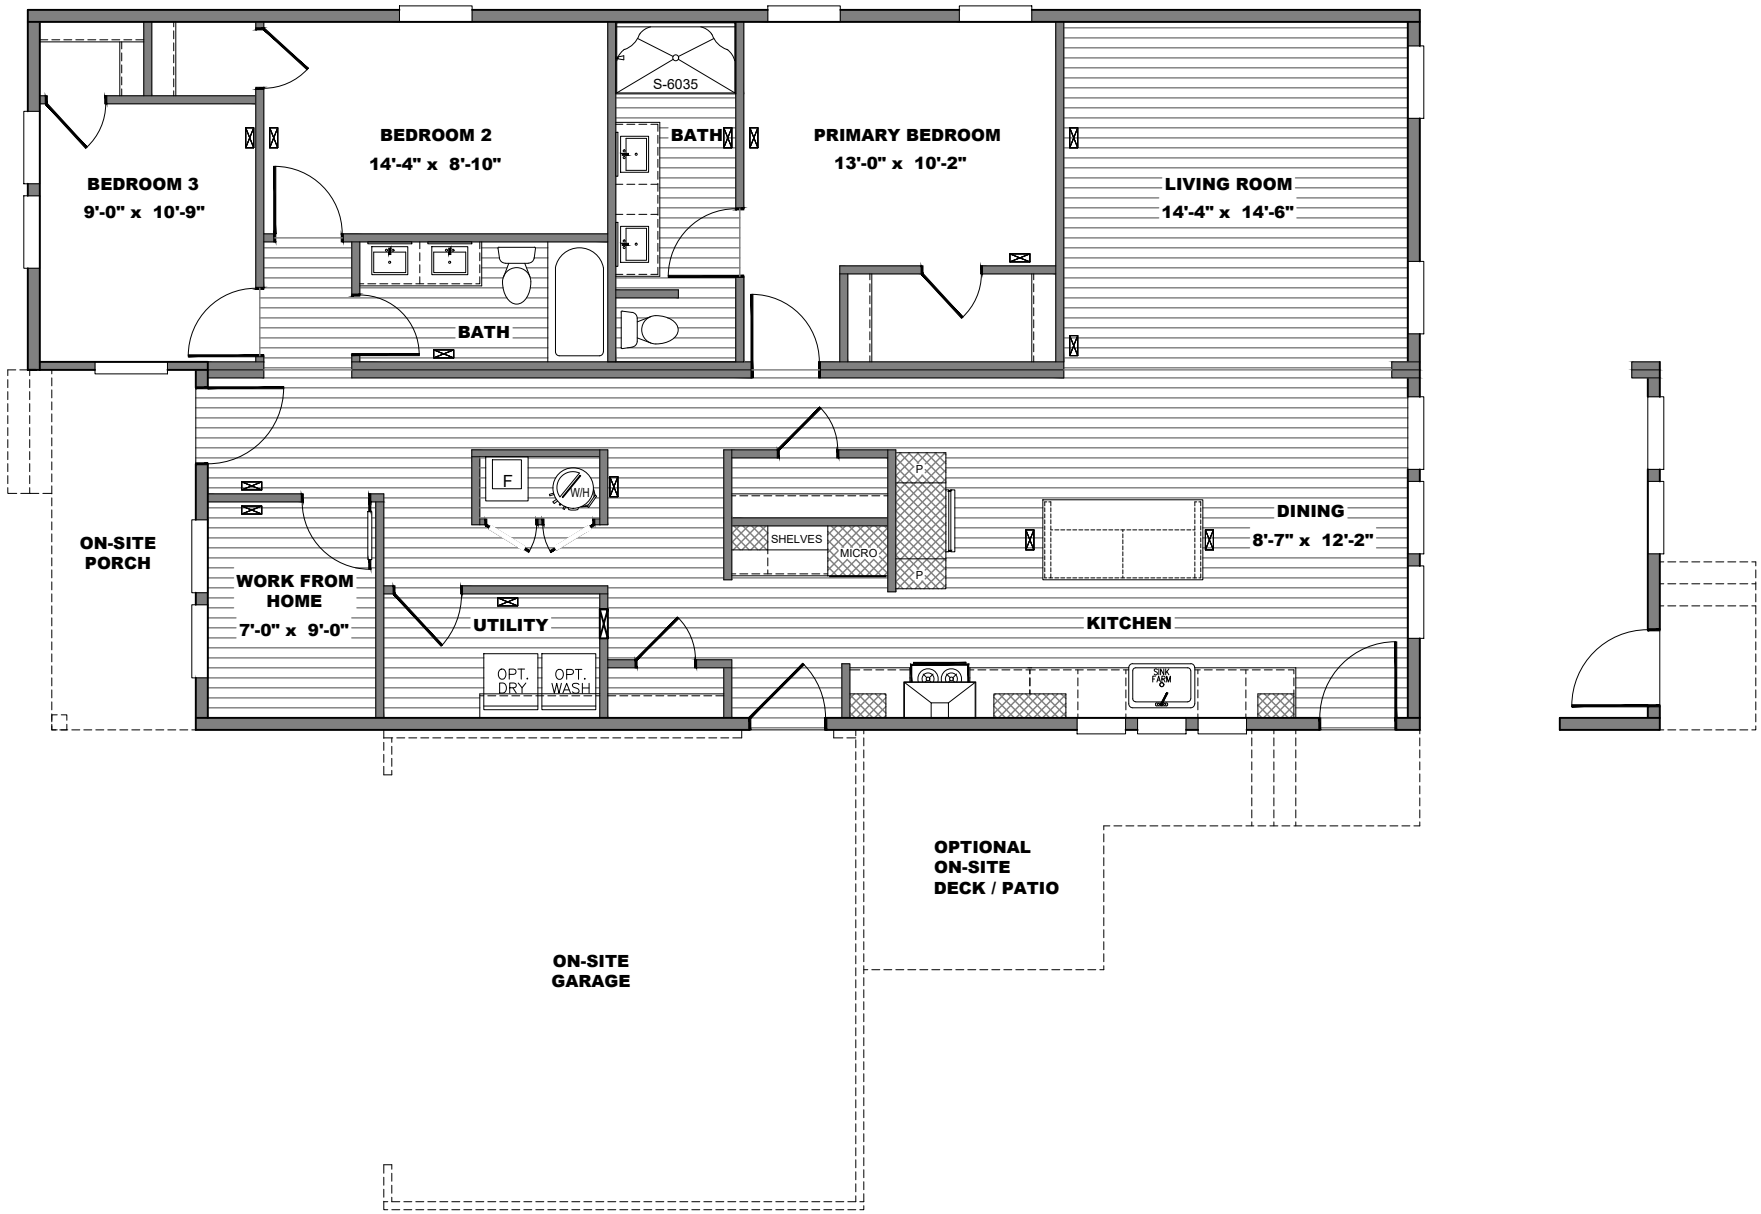

MODEL #CrossMod-3258-32-2_Magnolia_R SQ.FT. 1,635 DRAWING # CROSSMOD-3258-32-2_MAGNOLIA_R

File Path:B:\Architecture\CrossMod\DWG Files\3258_MAGNOLIA\CrossMod--3258-32-2_Magnolia_R.dwg, Last Saved By:Hutsella, Saved Date:9/28/2023 11:27 AM, Date Printed:9/28/23 12:28 PM

"CrossMod_Magnolia_R"

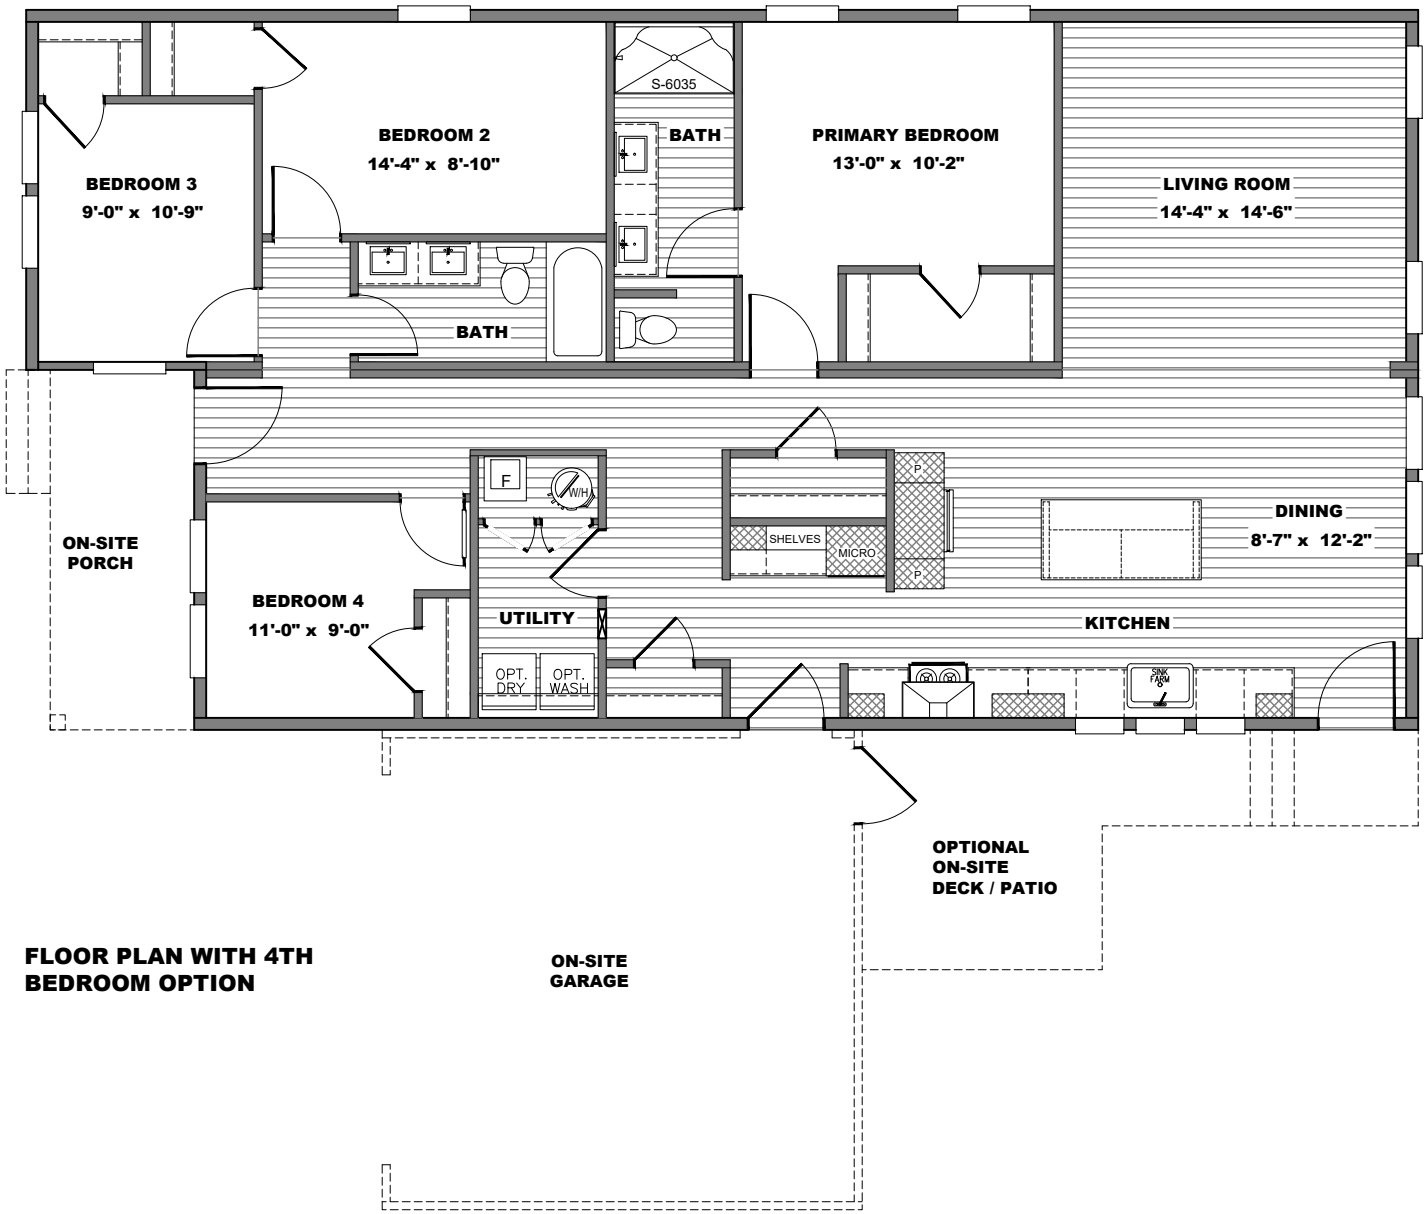


FLOOR PLAN WITH 4TH BEDROOM OPTION

MODEL #CrossMod-3258-32-2_Magnolia_R SQ.FT. 1,635 DRAWING # CROSSMOD-3258-32-2_MAGNOLIA_R

File Path:B:\Architecture\CrossMod\DWG Files\3258_MAGNOLIA\CrossMod--3258-32-2_Magnolia_R.dwg, Last Saved By:Hutsella, Saved Date:9/28/2023 11:27 AM, Date Printed:9/28/23 12:28 PM

"CrossMod_Magnolia_R"

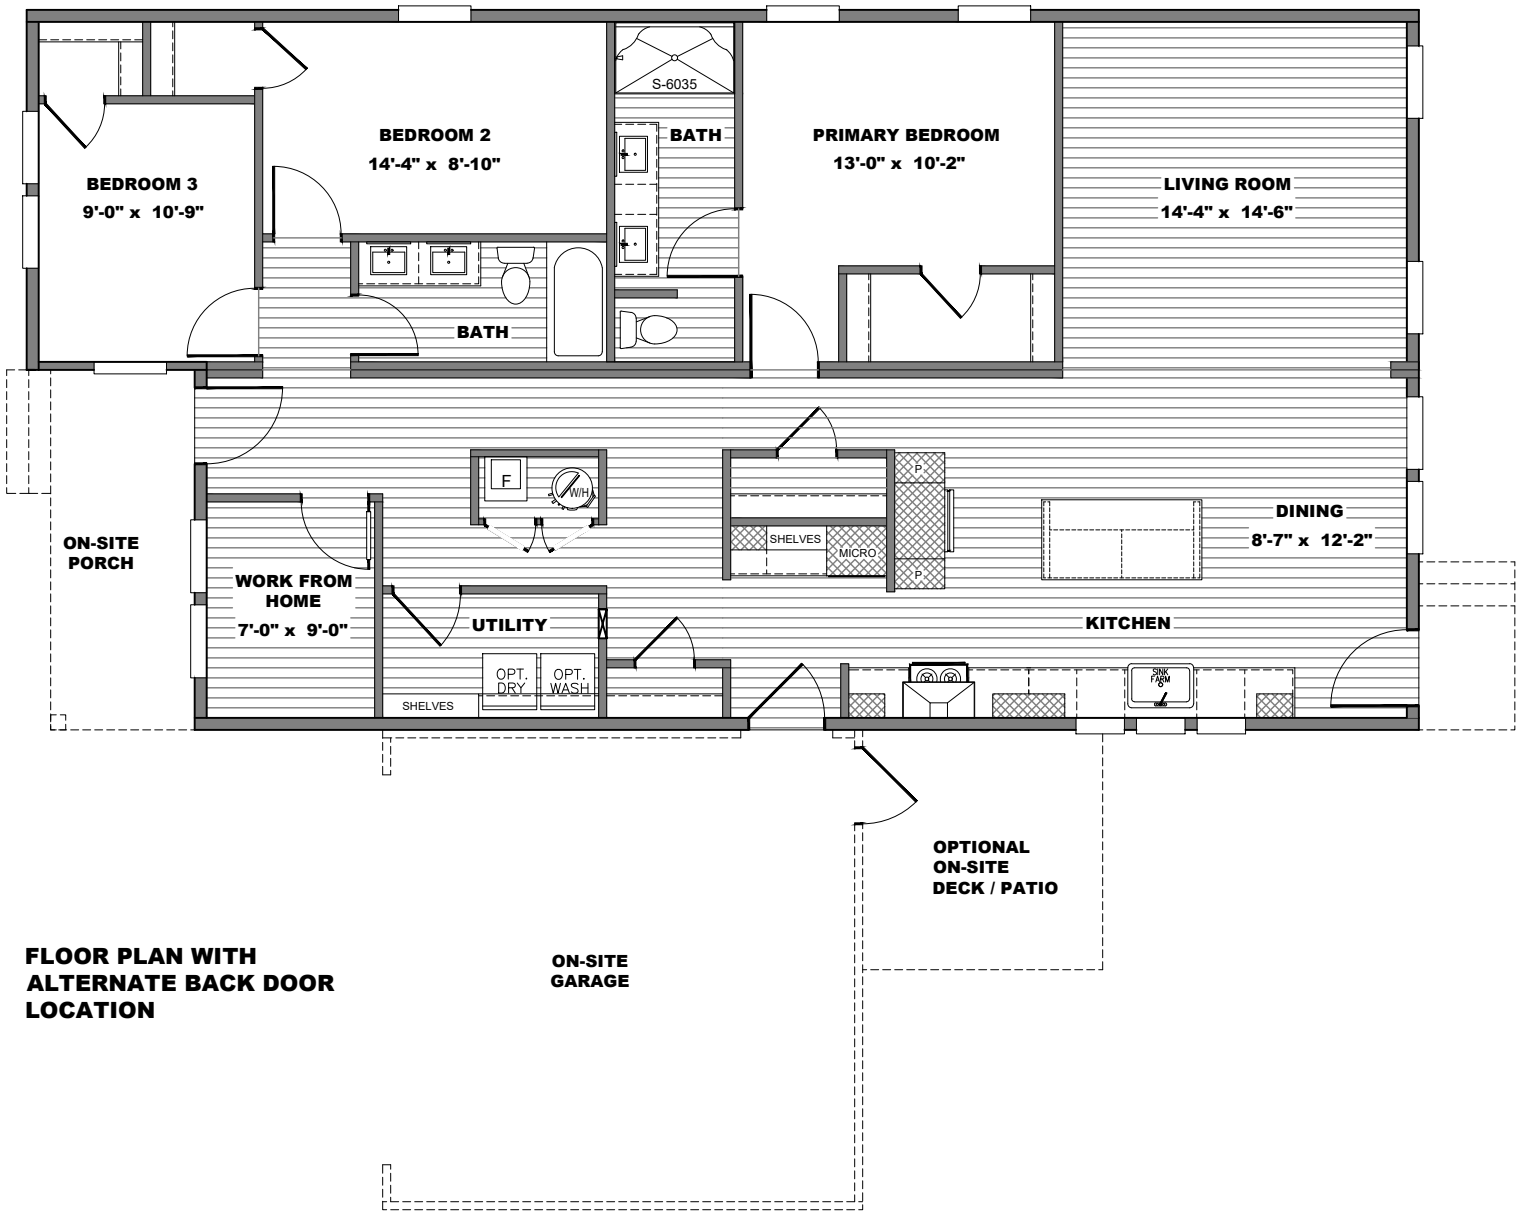


FLOOR PLAN WITH ALTERNATE BACK DOOR LOCATION

MODEL #CrossMod-3258-32-2_Magnolia_R SQ.FT. 1,635 DRAWING # CROSSMOD-3258-32-2_MAGNOLIA_R

File Path:B:\Architecture\CrossMod\DWG Files\3258_MAGNOLIA\CrossMod--3258-32-2_Magnolia_R.dwg, Last Saved By:Hutsella, Saved Date:9/28/2023 11:27 AM, Date Printed:9/28/23 12:28 PM

"CrossMod_Magnolia_R"

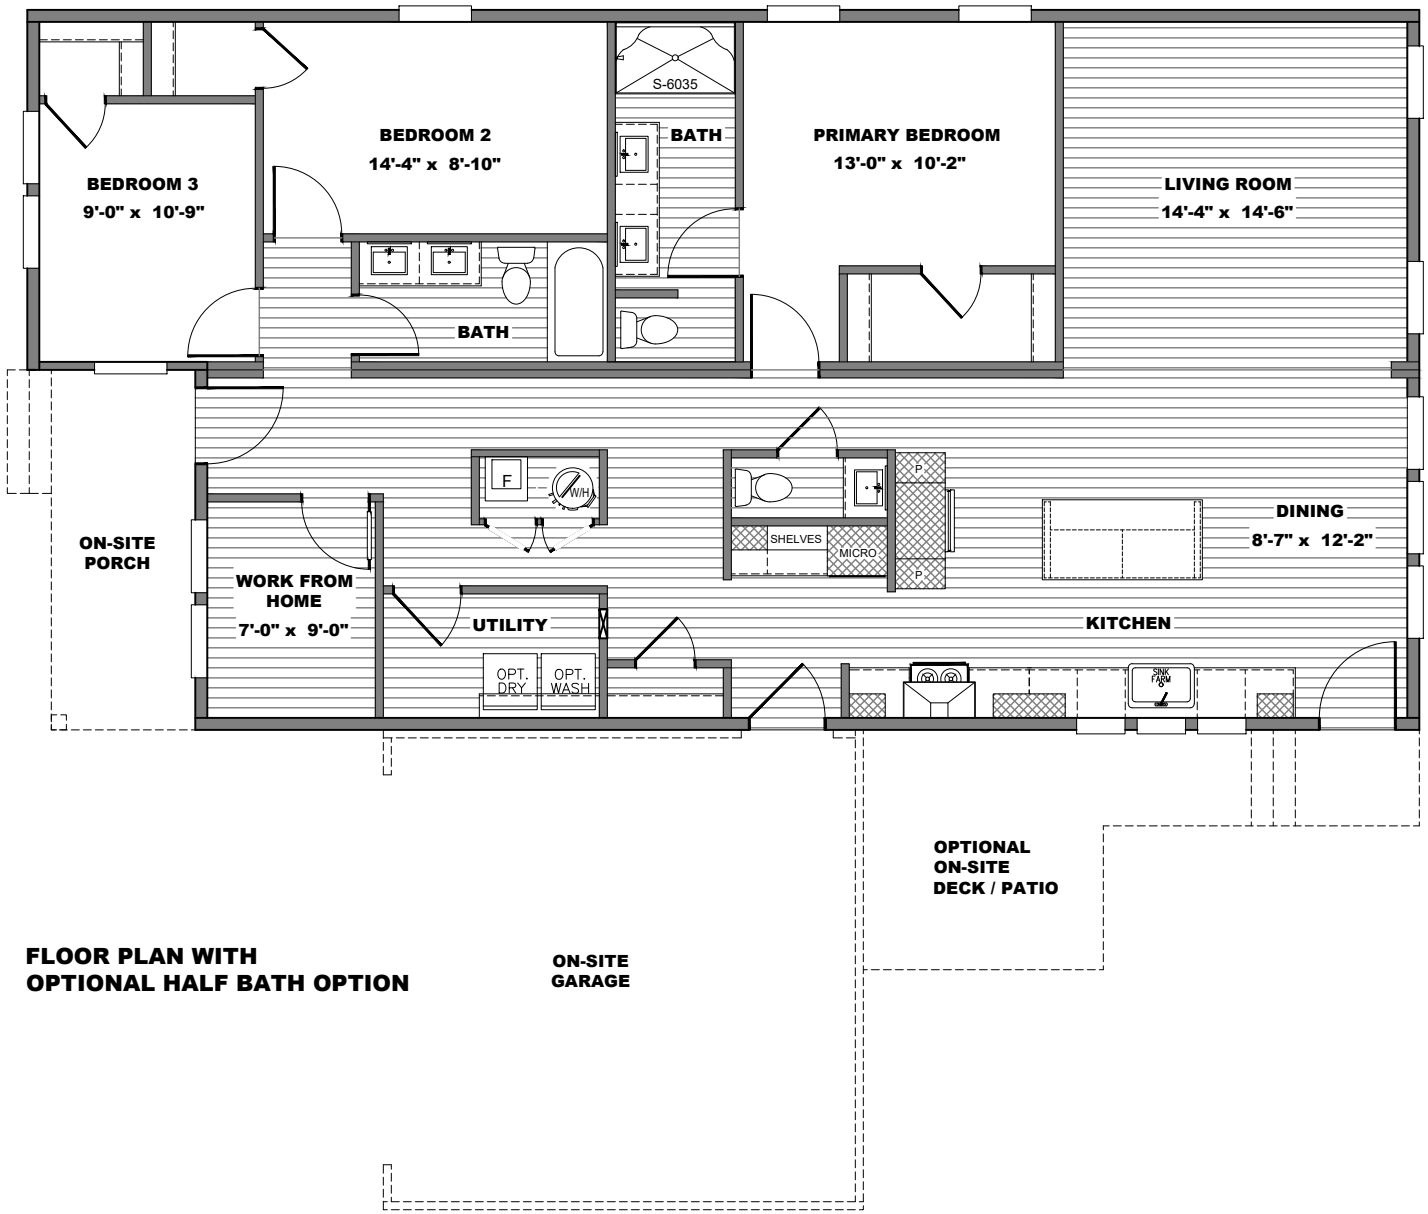

FLOOR PLAN WITH
OPTIONAL HALF BATH OPTION

MODEL #CrossMod-3258-32-2_Magnolia_R SQ.FT. 1,635 DRAWING # CROSSMOD-3258-32-2_MAGNOLIA_R

File Path:B:\Architecture\CrossMod\DWG Files\3258_MAGNOLIA\CrossMod--3258-32-2_Magnolia_R.dwg, Last Saved By:Hutsella, Saved Date:9/28/2023 11:27 AM, Date Printed:9/28/23 12:28 PM