

INDEX

A0.0	COVER SHEET
A1.0	FLOOR PLAN
A1.1	LIGHTING AND FLOOR REGISTER LAYOUT
A2.0	ELEVATIONS - STANDARD
A3.0	INTERIOR DETAILS - KITCHEN
A3.1	INTERIOR DETAILS - KITCHEN
A3.2	INTERIOR DETAILS - BATHS
A3.3	INTERIOR DETAILS - MISC
A4.0	SALESLIT PRINT SALESLIT

GENERAL NOTES

1. THIS PACKAGE IS INTENDED TO RELAY DESIGN INTENT AND IS NOT FOR CONSTRUCTION.
2. PLEASE CONTACT ANDY HUTSELL AT ANDY.HUTSELL@CLAYTONHOMES.COM WITH QUESTIONS REGARDING THESE DRAWINGS.

SYMBOLS AND ABBREVIATIONS


CLG	CEILING
DR	DOOR
EF	EXHAUST FAN
FLR	FLOOR
MNT	MOUNT
OPT	OPTIONAL
RAG	RETURN AIR GRILLE
SEP	STANDARD ELECTRIC PANEL
SGD	SLIDING GLASS DOOR

Clayton Built

MODEL NAME: CrossMod_Belmont_R
MODEL NO.: CrossMod-3260-32-1_Belmont_R
BOX SIZE: 32' x 60'
MODEL SQ. FT.: 1,620

DATE PRINTED: 9/26/2023
SCALE: N.T.S. * UNLESS OTHERWISE NOTED
PLAN NO.: CrossMod-3260-32-1_Belmont_R
SHEET NAME: COVER SHEET
SHEET NO.: A0.0.

File Path:B:\Architecture\CrossMod\DWG Files\3260_BELMONT\CrossMod-3260-32-1_Belmont_R.dwg, Last Saved By:Hutsella, Saved Date:9/26/2023 3:21 PM

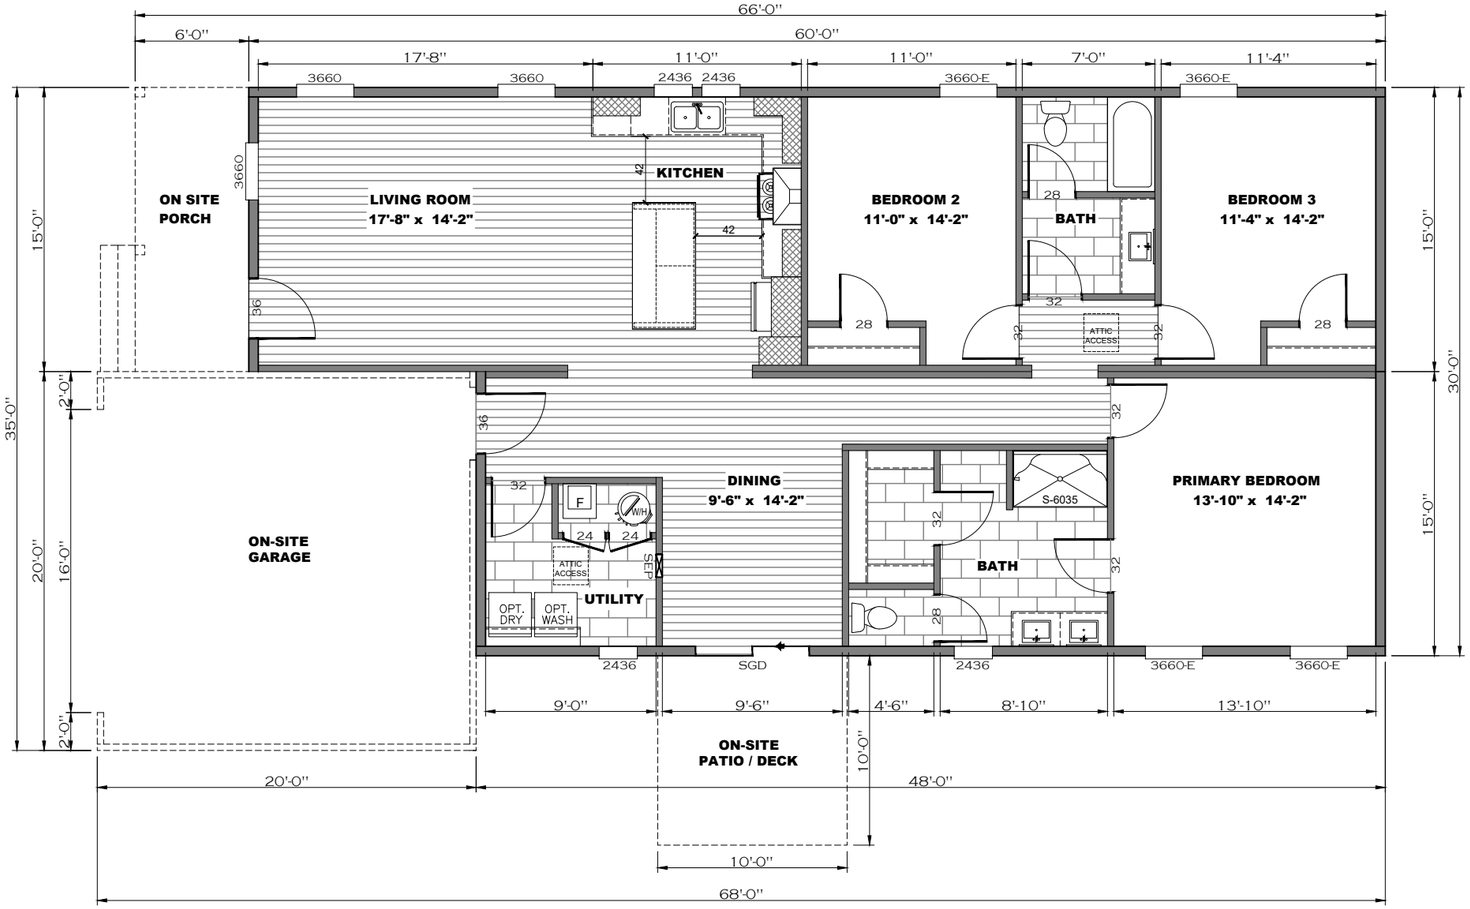

FLOOR PLAN

Clayton Built

MODEL NAME
CrossMod_Belmont_R

MODEL NO.
CrossMod-3260-32-1_Belmont_R

BOX SIZE
32' x 60'

MODEL SQ. FT.
1,620

DATE PRINTED
9/26/2023


SCALE
1/8"=1'
* UNLESS OTHERWISE NOTED

PLAN NO.
CrossMod--3260-32-1_Belmont_R

SHEET NAME
FLOOR PLAN

SHEET NO.
A1.0.

File Path:B:\Architecture\CrossMod\DWG Files\3260_BELMONT\CrossMod--3260-32-1_Belmont_R.dwg, Last Saved By:Hutsella, Saved Date:9/26/2023 3:21 PM

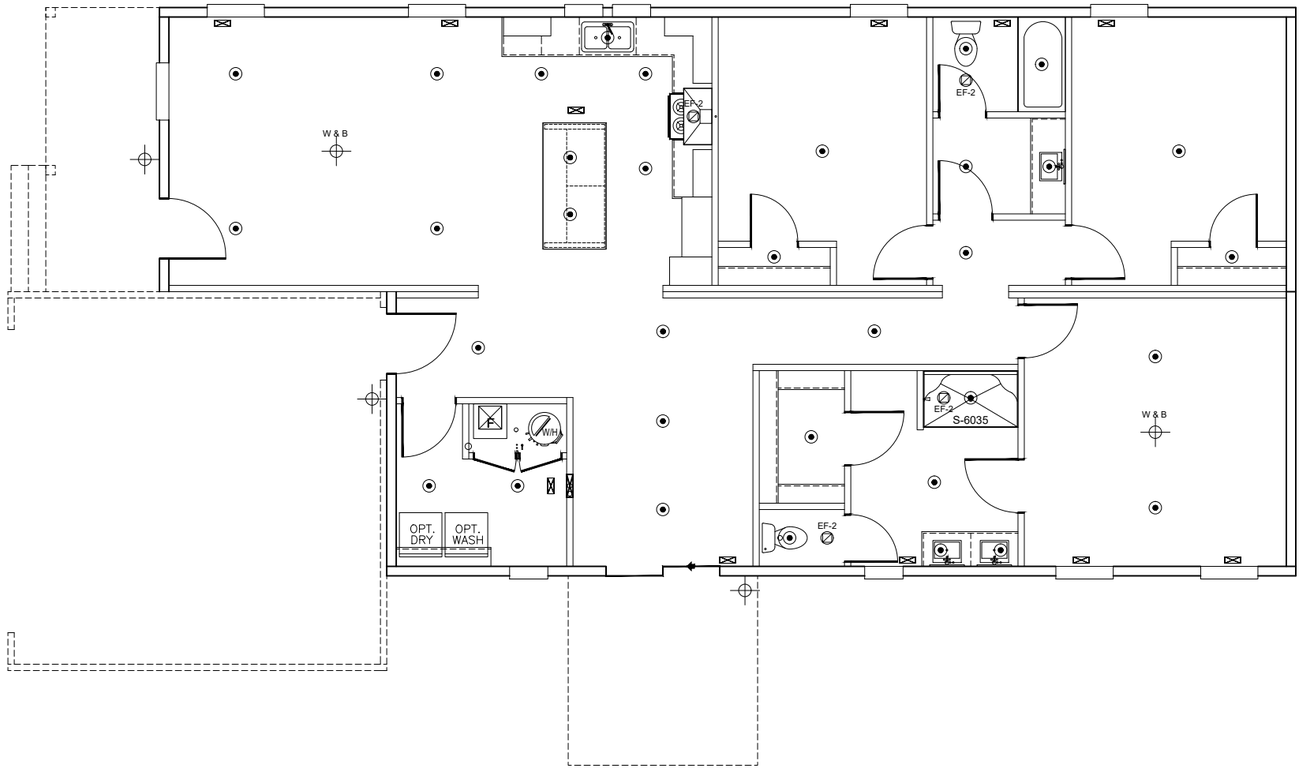

LIGHTING AND FLOOR REGISTER LAYOUT

SYMBOLS LEGEND	
W & B	OPT. CEILING FAN or WIRE & BRACE
	WALL OR CEILING MNT FIXTURE
	CAN LIGHT
EF-2	BATH FAN
	HVAC REGISTER
F	HVAC FURNACE
WH	WATER HEATER


NOTES:
1. ALL SYMBOLS MAY NOT BE APPLICABLE TO ALL PROJECTS.

Clayton Built


MODEL NAME: CrossMod_Belmont_R
MODEL NO.: CrossMod-3260-32-1_Belmont_R
BOX SIZE: 32' x 60'
MODEL SQ. FT.: 1,620

DATE PRINTED: 9/26/2023
SCALE: 1/8"=1' * UNLESS OTHERWISE NOTED
PLAN NO.: CrossMod--3260-32-1_Belmont_R
SHEET NAME: ELEC. PLAN
SHEET NO.: A1.1.


File Path:B:\Architecture\CrossMod\DWG Files\3260_BELMONT\CrossMod--3260-32-1_Belmont_R.dwg, Last Saved By:Hutsella, Saved Date:9/26/2023 3:21 PM

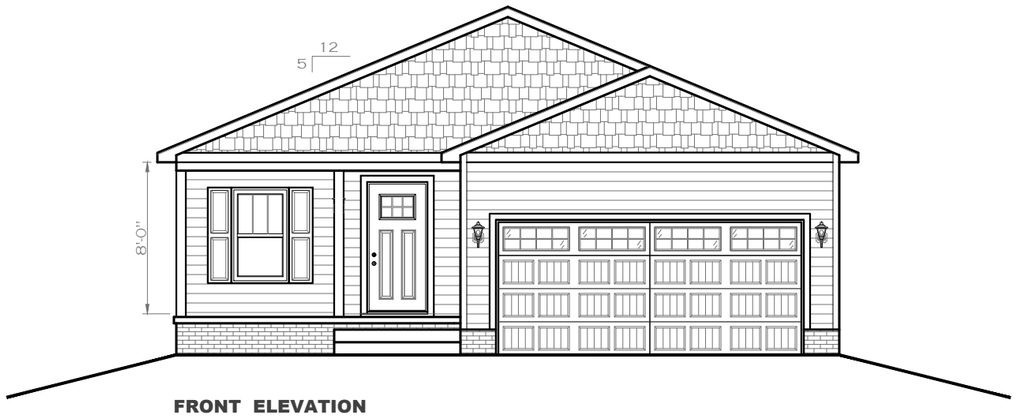

FRONT ELEVATION

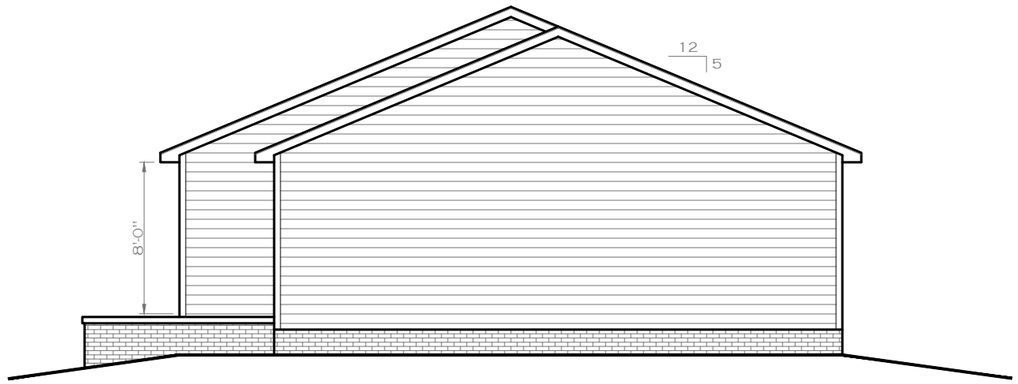

REAR ELEVATION

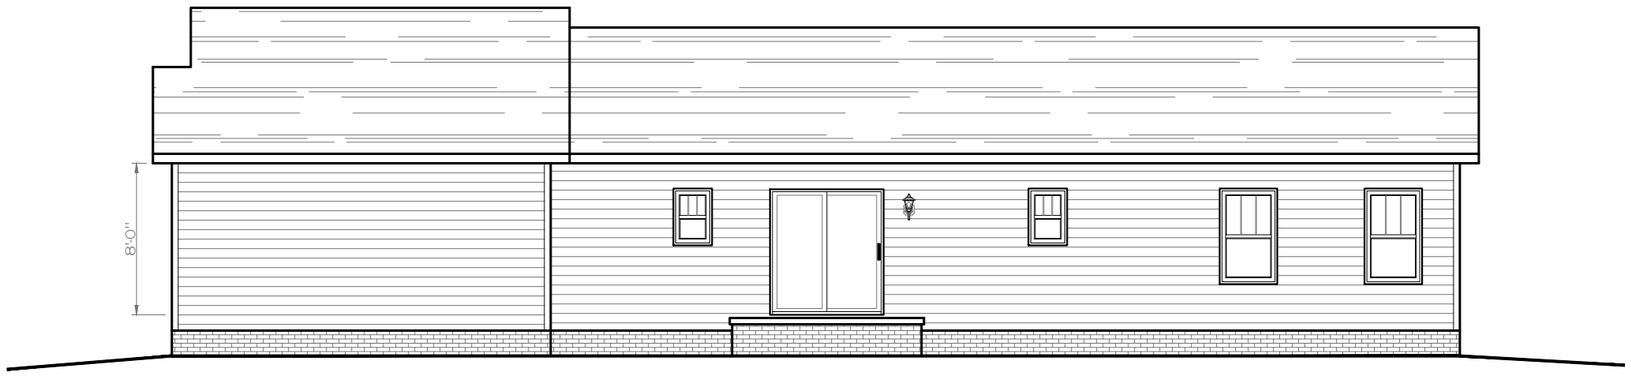

RIGHT SIDE ELEVATION



LEFT SIDE ELEVATION

Clayton Built

MODEL NAME
CrossMod_Belmont_R

MODEL NO.
CrossMod-3260-32-1_Belmont_R

BOX SIZE
32' x 60'

MODEL SQ. FT.
1,620

DATE PRINTED
9/26/2023


SCALE
1/8"=1'
* UNLESS OTHERWISE NOTED

PLAN NO.
CrossMod--3260-32-1_Belmont_R


SHEET NAME
EXTERIOR ELEVATION

SHEET NO.
A2.0.

File Path:B:\Architecture\CrossMod\DWG Files\3260_BELMONT\CrossMod--3260-32-1_Belmont_R.dwg, Last Saved By:Hutsella, Saved Date:9/26/2023 3:21 PM

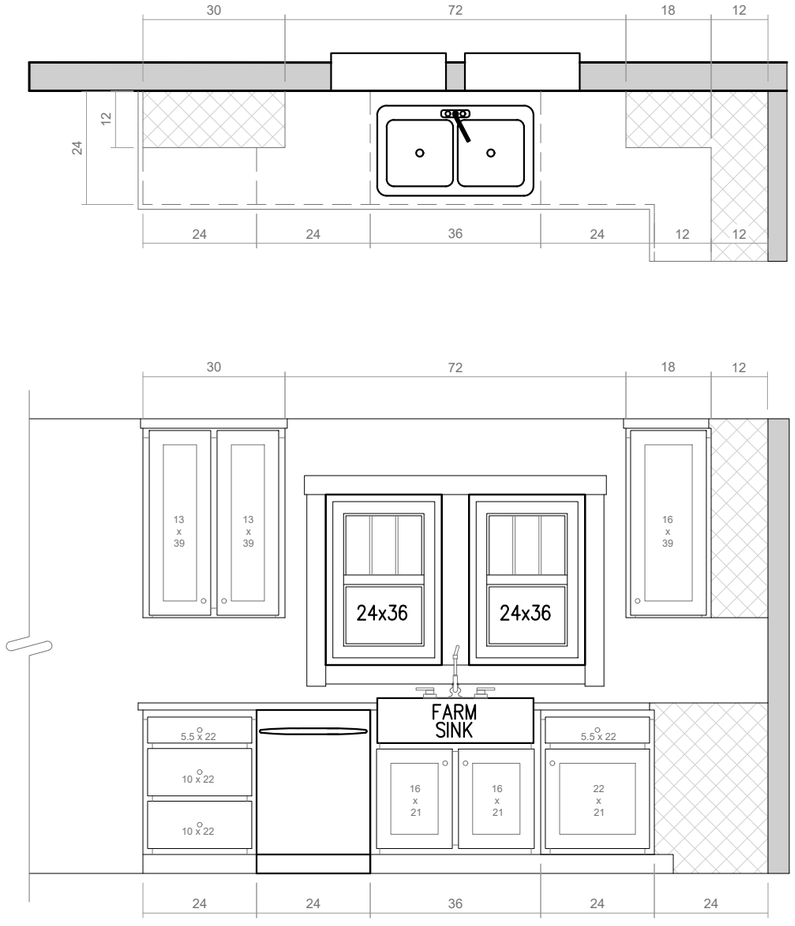

KITCHEN ELEVATION @ SINK / DISHWASHER

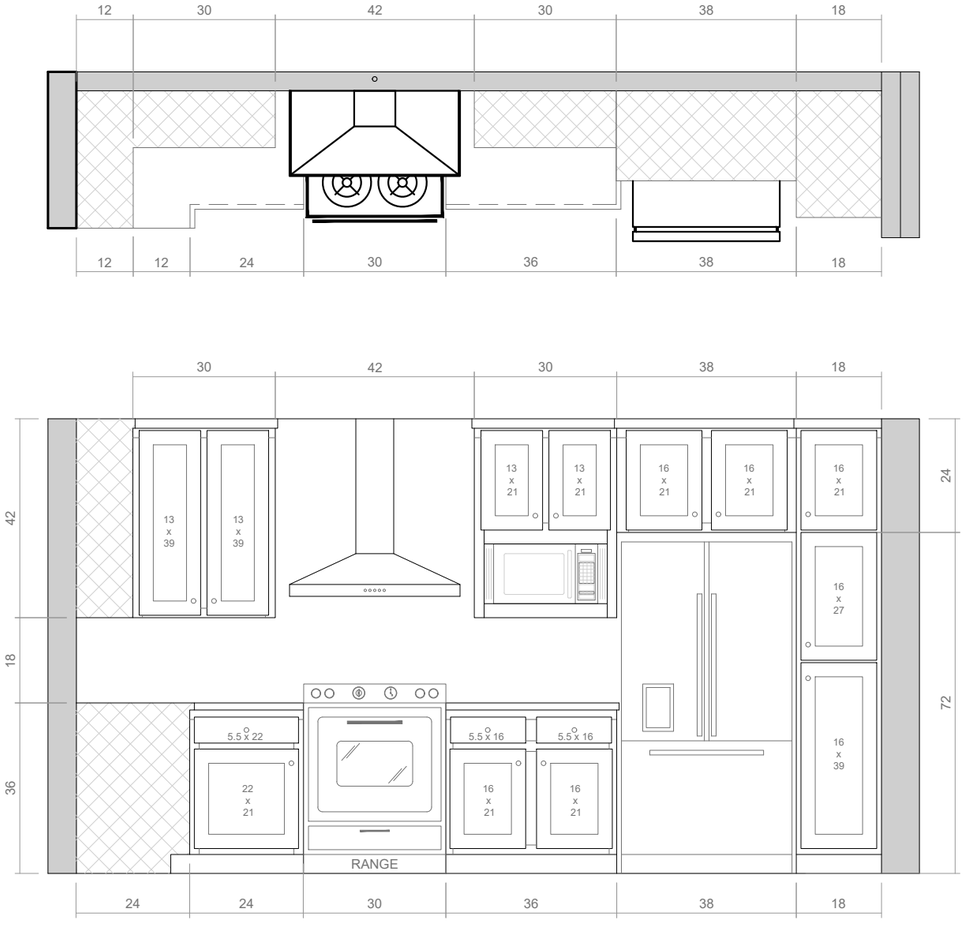

KITCHEN ELEVATION @ OVEN / REFRIDGERATOR

Clayton Built

MODEL NAME
CrossMod_Belmont_R

MODEL NO.
CrossMod-3260-32-1_Belmont_R

BOX SIZE
32' x 60'

MODEL SQ. FT.
1,620

DATE PRINTED
9/26/2023


SCALE
3/8"=1'
* UNLESS OTHERWISE NOTED

PLAN NO.
CrossMod--3260-32-1_Belmont_R


SHEET NAME
CABINETS
KITCHEN

SHEET NO.
A3.0.

File Path:B:\Architecture\CrossMod\DWG Files\3260_BELMONT\CrossMod--3260-32-1_Belmont_R.dwg, Last Saved By:Hutsella, Saved Date:9/26/2023 3:21 PM

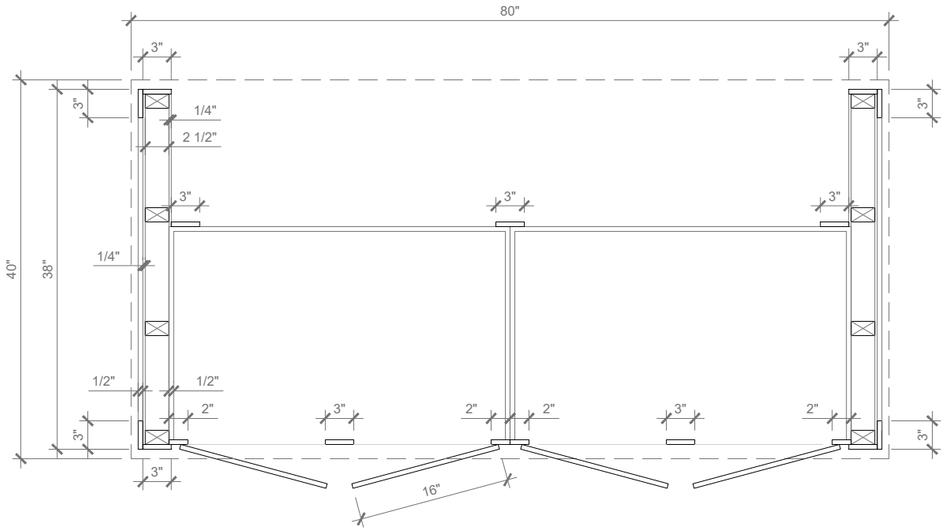

ISLAND PLAN/SECTION
$\frac{3}{4}$" = 1'-0"

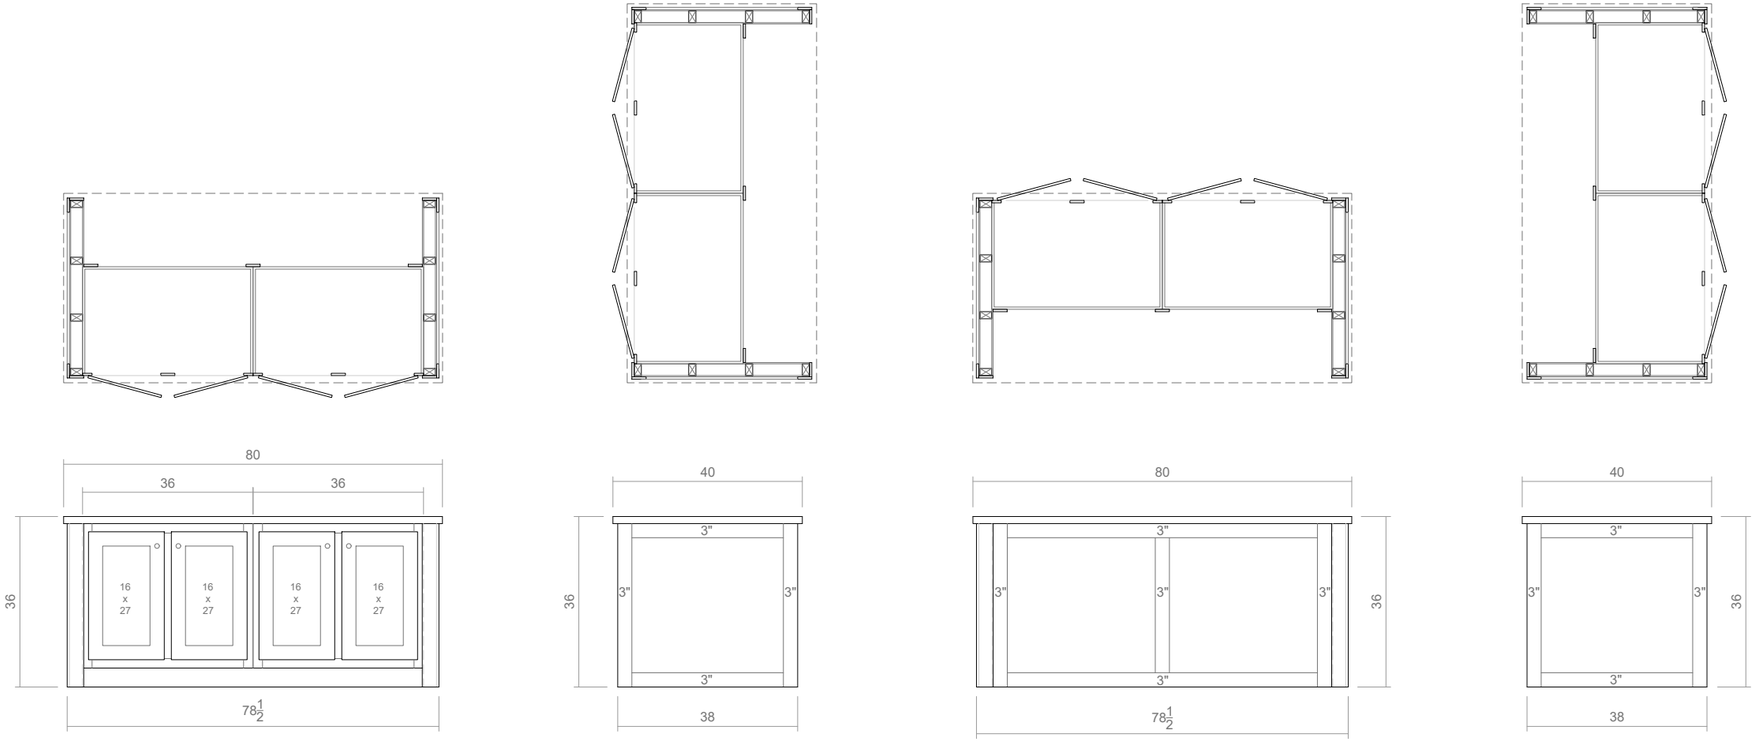


ISLAND ELEVATIONS
$\frac{3}{8}$" = 1'-0"

Clayton Built

MODEL NAME: CrossMod_Belmont_R
MODEL NO.: CrossMod-3260-32-1_Belmont_R
BOX SIZE: 32' x 60'
MODEL SQ. FT.: 1,620


DATE PRINTED: 9/26/2023
SCALE: VARIES
* UNLESS OTHERWISE NOTED
PLAN NO.: CrossMod--3260-32-1_Belmont_R
SHEET NAME: CABINETS KITCHEN
SHEET NO.: A3.1.


File Path:B:\Architecture\CrossMod\DWG Files\3260_BELMONT\CrossMod--3260-32-1_Belmont_R.dwg, Last Saved By:Hutsella, Saved Date:9/26/2023 3:21 PM

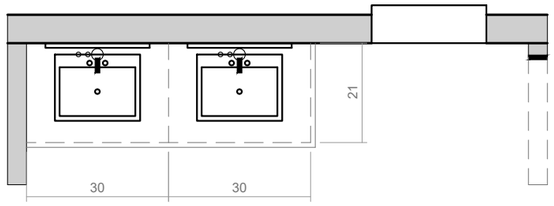



PRIMARY BATH ELEVATION

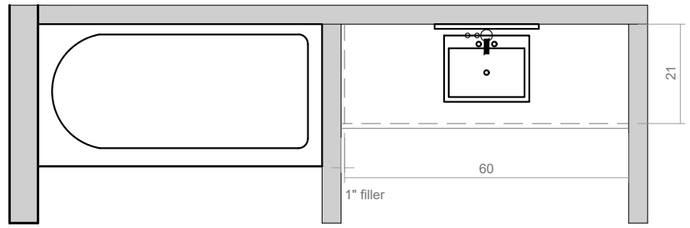

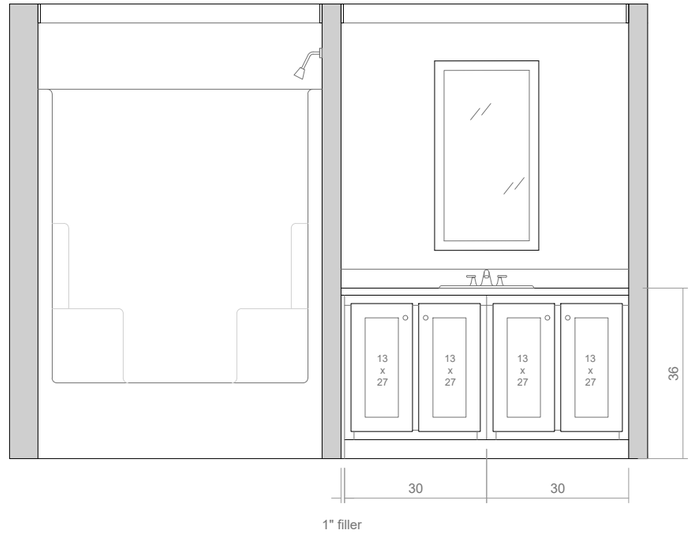


HALL BATH ELEVATION


Clayton Built

MODEL NAME: CrossMod_Belmont_R
MODEL NO.: CrossMod-3260-32-1_Belmont_R
BOX SIZE: 32' x 60'
MODEL SQ. FT.: 1,620


DATE PRINTED: 9/26/2023
SCALE: 3/8"=1'
* UNLESS OTHERWISE NOTED
PLAN NO.: CrossMod--3260-32-1_Belmont_R
SHEET NAME: CABINETS BATH
SHEET NO.: A3.2


File Path:B:\Architecture\CrossMod\DWG Files\3260_BELMONT\CrossMod--3260-32-1_Belmont_R.dwg, Last Saved By:Hutsella, Saved Date:9/26/2023 3:21 PM

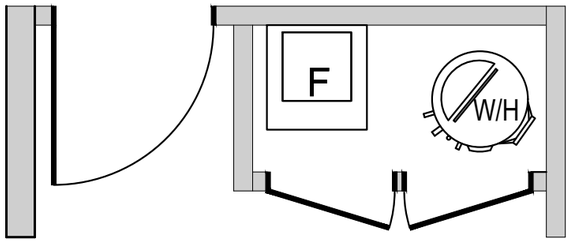

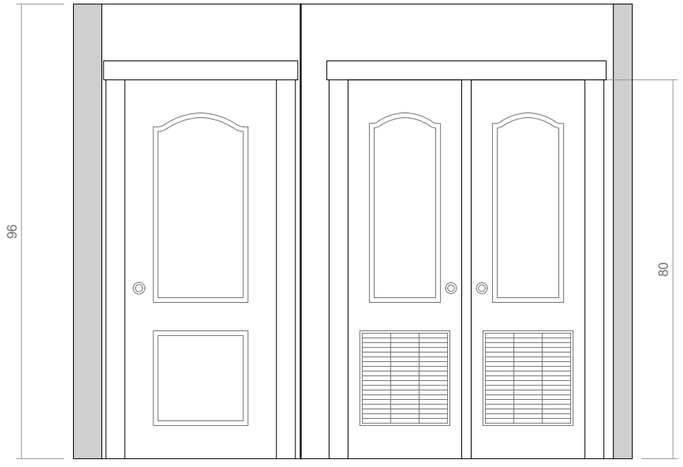



INTERIOR ELEVATION @ UTILITY CLOSET

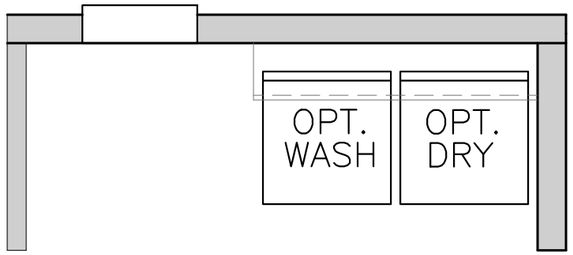

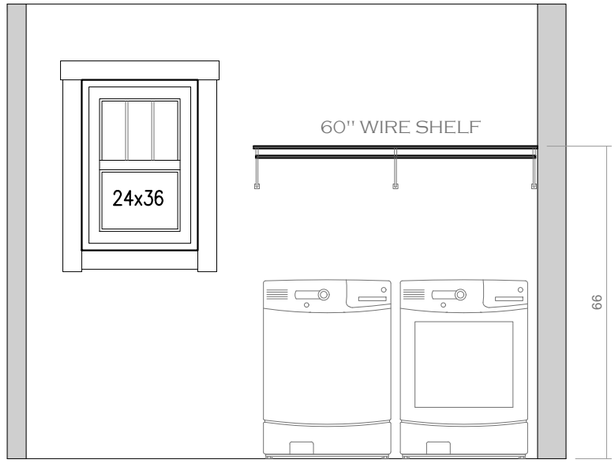

INTERIOR ELEVATION @ WASHER / DRYER

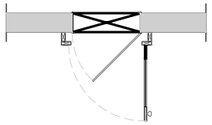

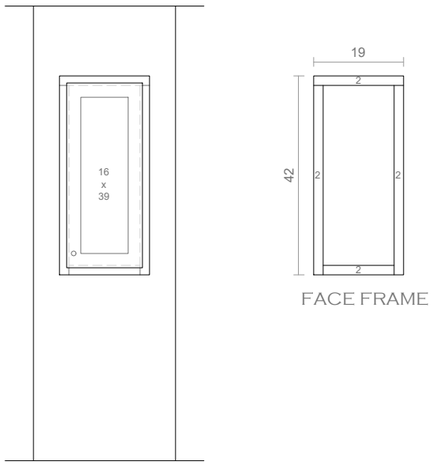


PROPOSED CABINET DOOR COVER @ PANEL BOX (NEEDS TO BE PROTOTYPED)

Clayton Built

MODEL NAME: CrossMod_Belmont_R
MODEL NO.: CrossMod-3260-32-1_Belmont_R
BOX SIZE: 32' x 60'
MODEL SQ. FT.: 1,620

DATE PRINTED: 9/26/2023
SCALE: 3/8"=1'
* UNLESS OTHERWISE NOTED
PLAN NO.: CrossMod-3260-32-1_Belmont_R
SHEET NAME: MISC. DETAILS
SHEET NO.: A3.3.

File Path:B:\Architecture\CrossMod\DWG Files\3260_BELMONT\CrossMod-3260-32-1_Belmont_R.dwg, Last Saved By:Hutsella, Saved Date:9/26/2023 3:21 PM

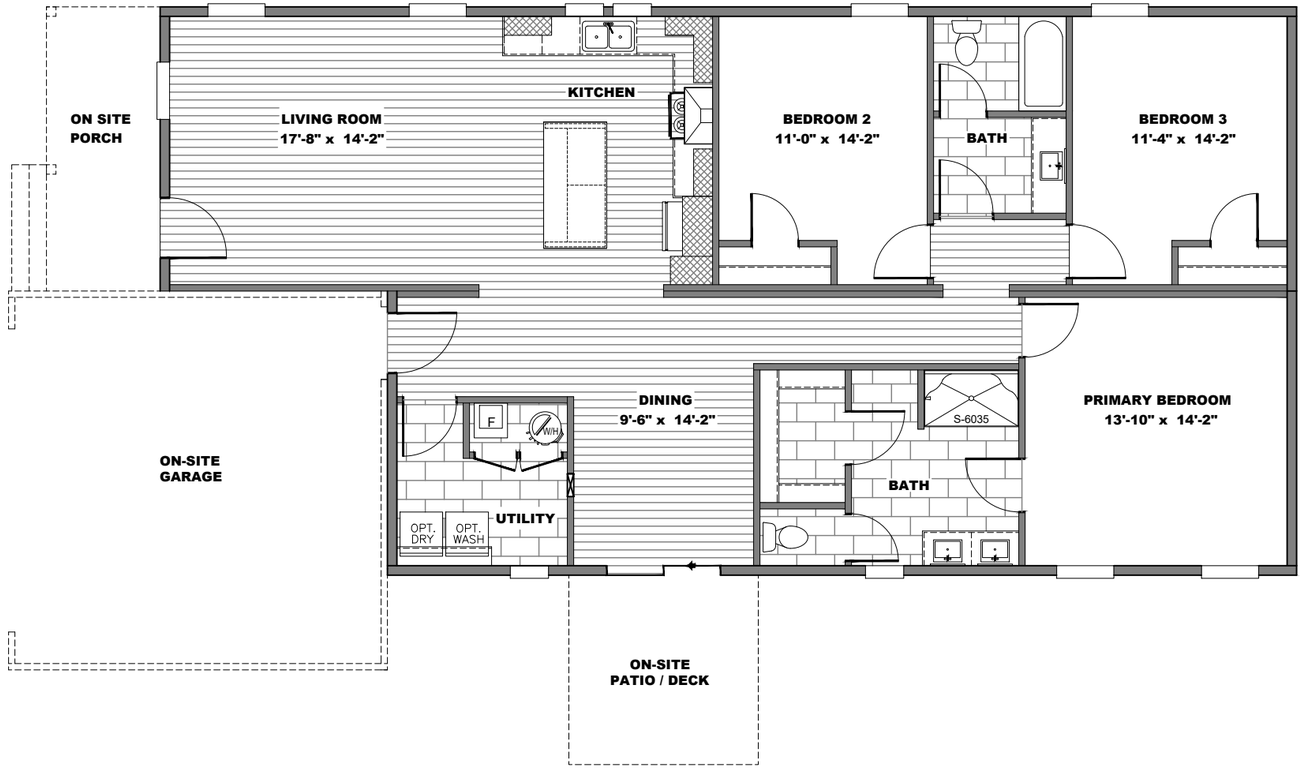

Clayton Built

MODEL NAME: CrossMod_Belmont_R

MODEL NO.: CrossMod-3260-32-1_Belmont_R

BOX SIZE: 32' x 60'

MODEL SQ. FT.: 1,620

DATE PRINTED: 9/26/2023

SCALE: 1/8"=1'

* UNLESS OTHERWISE NOTED


PLAN NO.: CrossMod-3260-32-1_Belmont_R

SHEET NAME: SALESLIT

SHEET NO.: A4.0.

File Path:B:\Architecture\CrossMod\DWG Files\3260_BELMONT\CrossMod-3260-32-1_Belmont_R.dwg, Last Saved By:Hutsella, Saved Date:9/26/2023 3:21 PM

"CrossMod_Belmont_R"

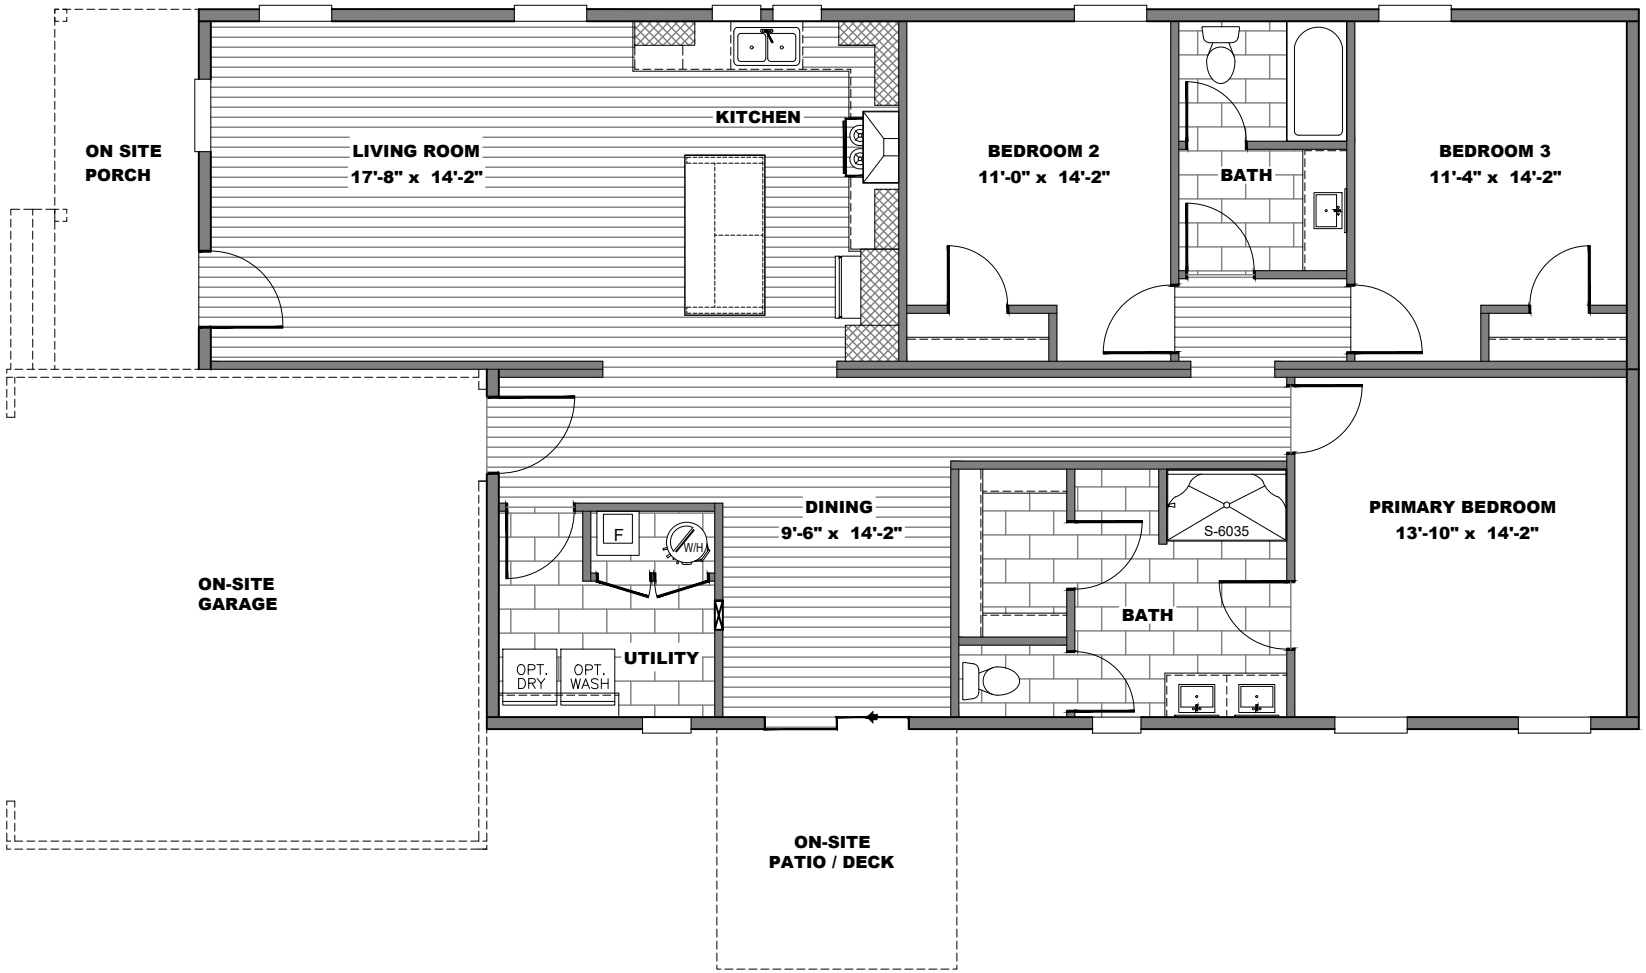

MODEL #CrossMod-3260-32-1_Belmont_R SQ.FT. 1,620 DRAWING # CROSSMOD-3260-32-1_BELMONT_R

File Path:B:\Architecture\CrossMod\DWG Files\3260_BELMONT\CrossMod--3260-32-1_Belmont_R.dwg, Last Saved By:Hutsella, Saved Date:9/26/2023 3:21 PM, Date Printed:9/26/23 3:23 PM